

A

B

C

D

E


F

G

H

DESPIECE - EXTINTOR ABC 100 KG SOBRE RUEDAS

Isometría explosionada por subconjunto, escala 1:10. Globo = posición del plano FL_MAT_ABC_100kg = código ABC100-NN

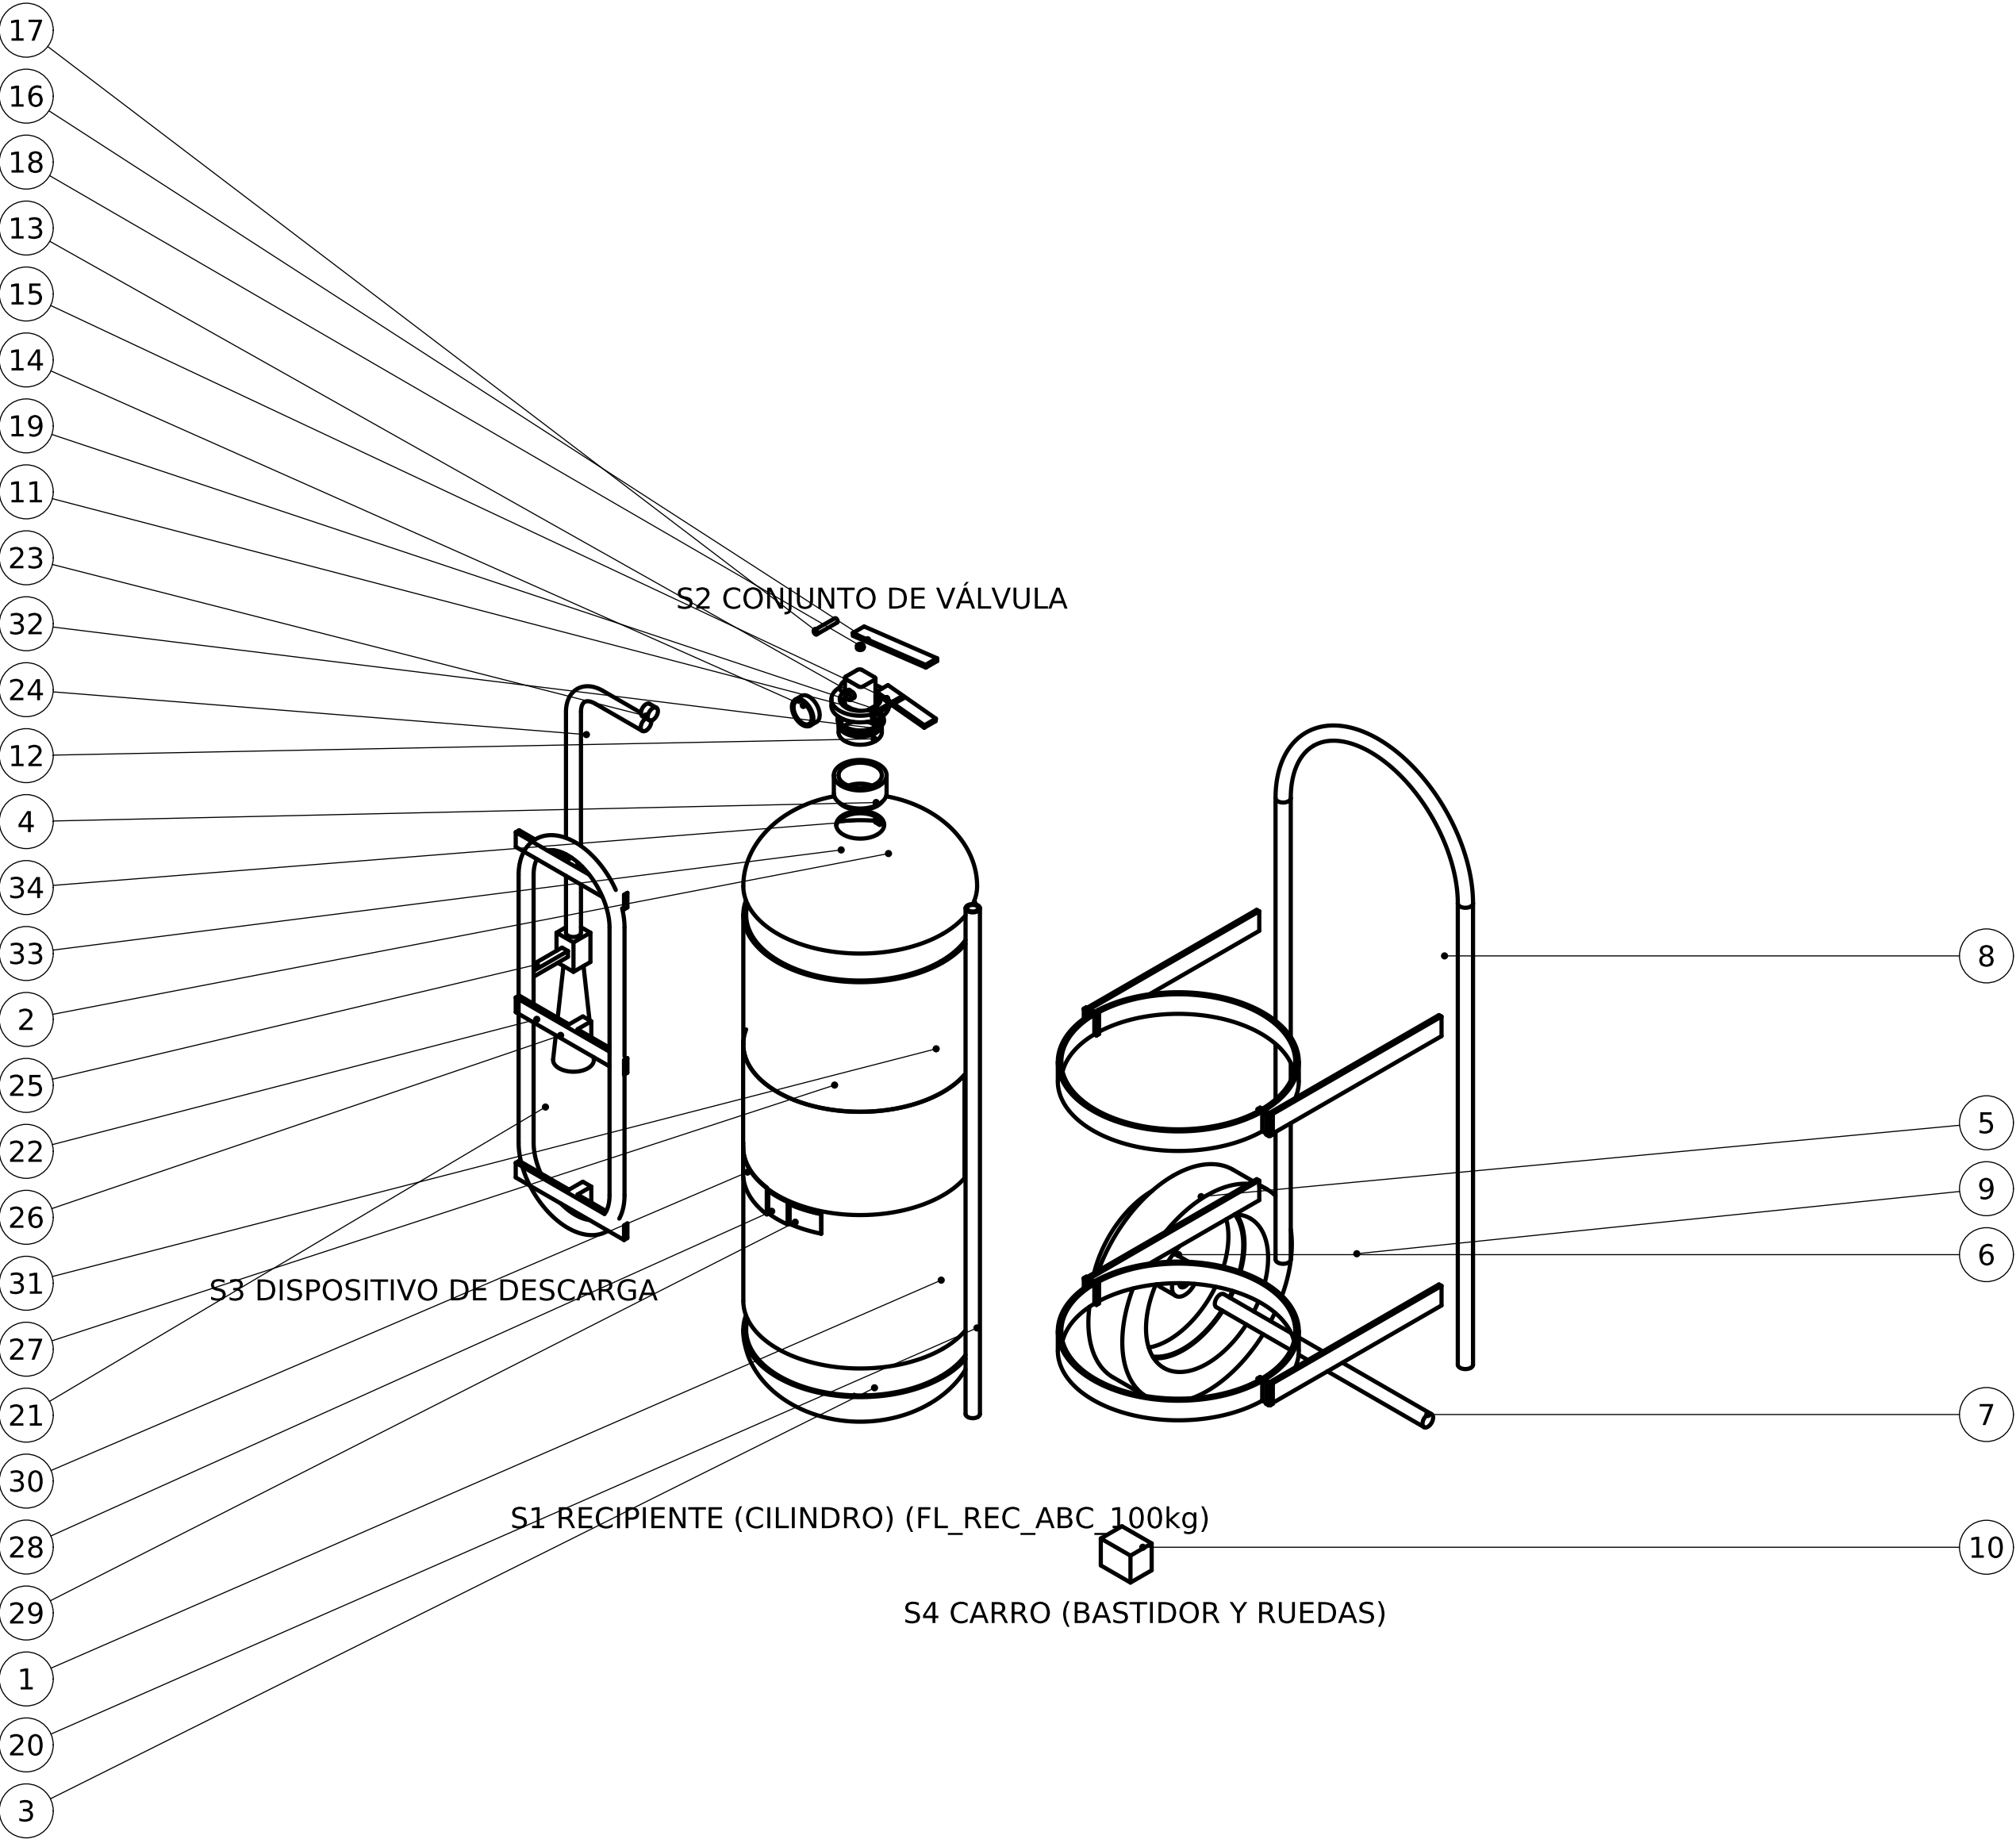

LISTA DE DESPIECE - BOM FL_MAT_ABC_100kg

Glo.	Código BOM	Denominación	Cant.	Material
	FL_REC_ABC_100kg	RECIPIENTE (CILINDRO)		
1	ABC100-01	Cuerpo (virola)	1	Chapa LAC IRAM-IAS U 500-04 e=
2	ABC100-02	Cúpula	1	Chapa LAC IRAM-IAS U 500-04 e=
3	ABC100-03	Fondo	1	Chapa LAC IRAM-IAS U 500-04 e=
4	ABC100-04	Cuello roscado	1	Acero SAE 1010
—	ABC100-C1	Alambre de soldadura ER70S-6 Ø0,9/1,2 (AWS A5.	1,0305 kg	ER70S-6
—	ABC100-C2	Gas de protección M20: Ar + 8 % CO ₂ (ARCAL Spe	None L	EN ISO 14175 M20-ArC-8
—	ABC100-C4	Servicio de pintura en polvo al horno, rojo 03	1	Servicio tercerizado
—	ABC100-C5	Varilla de refuerzo interior longitudinal	None	Barra de acero
	ABC100-S2	CONJUNTO DE VÁLVULA		
11	ABC100-11	Collarín de válvula	1	Latón forjado
12	ABC100-12	Espiga roscada	1	Latón forjado
13	ABC100-13	Cuerpo de válvula	1	Latón forjado
14	ABC100-14	Manómetro	1	Comercial
15	ABC100-15	Manija de transporte	1	Chapa acero SAE 1010 pintada
16	ABC100-16	Manija de accionamiento	1	Chapa acero SAE 1010 pintada
17	ABC100-17	Eje de palanca	1	Acero inox. AISI 304
18	ABC100-18	Vástago	1	Latón
19	ABC100-19	Pasador de seguridad	1	Alambre acero inox. AISI 304
20	ABC100-20	Caño de pesca (sifón)	1	Tubo PVC rígido
32	ABC100-32	Junta tórica de asiento	1	NBR 70 Shore A
—	ABC100-K2	Válvula HZ armada de carro 50-70-100 kg	1	Latón forjado (HZ)
—	ABC100-V2	Resorte de retorno del vástago	1	Acero para resortes
—	ABC100-V3	Junta tórica del vástago	1	NBR 70 Shore A
	ABC100-S3	DISPOSITIVO DE DESCARGA		
21	ABC100-21	Manguera (tramo enrollado)	1	Caucho sintético
22	ABC100-22	Soporte de manguera	1	Planchuela acero SAE 1010
23	ABC100-23	Racor de manguera	1	Latón
24	ABC100-24	Manguera	1	Caucho sintético
25	ABC100-25	Válvula esférica	1	Latón cromado
26	ABC100-26	Tobera campana	1	Polipropileno
	ABC100-S4	CARRO (BASTIDOR Y RUEDAS)		
5	ABC100-05	Neumático macizo	2	Caucho
6	ABC100-06	Llanta con cubo	2	Chapa acero SAE 1010
7	ABC100-07	Eje de ruedas	1	Acero SAE 1045
8	ABC100-08	Bastidor	1	Caño acero SAE 1010 Ø25,4×1,6
9	ABC100-09	Sunchos de fijación	1	Planchuela acero SAE 1010
10	ABC100-10	Apoyo delantero	1	Chapa acero SAE 1010 plegada
—	ABC100-K4	Carro armado (bastidor, eje, ruedas, sunchos y	1	Acero / caucho
	ABC100-S5	CARGA: AGENTE EXTINTOR Y GAS IMPULSOR		
—	ABC100-A1	Polvo químico seco ABC 90 (Sello IRAM 3569, DE	100 kg	Polvo químico seco ABC 90 (Sel
—	ABC100-A2	Gas impulsor: N ₂	0,205 kg	N ₂
	ABC100-S6	IDENTIFICACIÓN Y PRECINTO		
27	ABC100-27	Etiqueta / placa de características	1	Vinilo autoadhesivo laminado
28	ABC100-28	Oblea de fabricación (PBA)	1	Papel de seguridad autodestruc
29	ABC100-29	Estampilla IRAM de conformidad	1	Provista por IRAM (Anexo R)
30	ABC100-30	Tarjeta de identificación AGC (CABA)	1	Etiqueta autoadhesiva emitida
31	ABC100-31	Etiqueta de n° de serie GS1	1	Poliéster autoadhesivo impreso
33	ABC100-33	Faja de garantía válvula-cuello	1	Vinilo destructible rayado roj
34	ABC100-34	Precinto de fábrica	1	Polipropileno color
	ABC100-S7	EMBALAJE		
—	ABC100-E1	Esquineros y funda de polietileno	1 jgo	PE / cartón
—	ABC100-E3	Pallet 1200 × 1000 (fracción)	1	Madera
—	ABC100-E4	Film stretch (fracción del pallet)	None kg	PE lineal 23 µm
—	ABC100-E5	Etiqueta de pallet (lote y destino, fracción)	1	Papel térmico

NOTAS

- 1) Lista completa con medidas, pesos, origen, operación y norma: salida/bom/FLAMA_BOM.xlsx, hoja FL_MAT_ABC_100kg.
- 2) «—» = ítem no dibujado (internos de válvula, carga, identificación, embalaje).
- 3) S1 en los ABC = recipiente FL_REC (mismo plano que el cilindro de venta suelta).
- 4) Ruedas: se dibujan ambas, el globo señala la derecha (cantidad 2).

	Fecha	Nombre	Propietario FLAMA S.A.		Reemplaza a / Reemplazado por	
Dibujó	28/09/26	T. Sinay			-	
Revisó			Denominación Despiece ABC 100 kg sobre ruedas Vista explosionada y lista multinivel (BOM)		Material	
Aprobó					Ver lista	
Escala	Método de proyección				Edición	Fecha de emisión
1:10	 ISO E		0	28/09/2026		
Tolerancias generales		Formato	Tipo de documento Plano de despiece		Hoja	Idioma
ISO 2768-m		A2			1 / 1	es
					N° de plano	
					FL_DES_ABC_100kg	