


DESPIECE - EXTINTOR ABC 100 KG SOBRE RUEDAS

Isometría explosionada por subconjunto, escala 1:10. Globo = posición del plano FL_MAT_ABC_100kg = código ABC100-NN

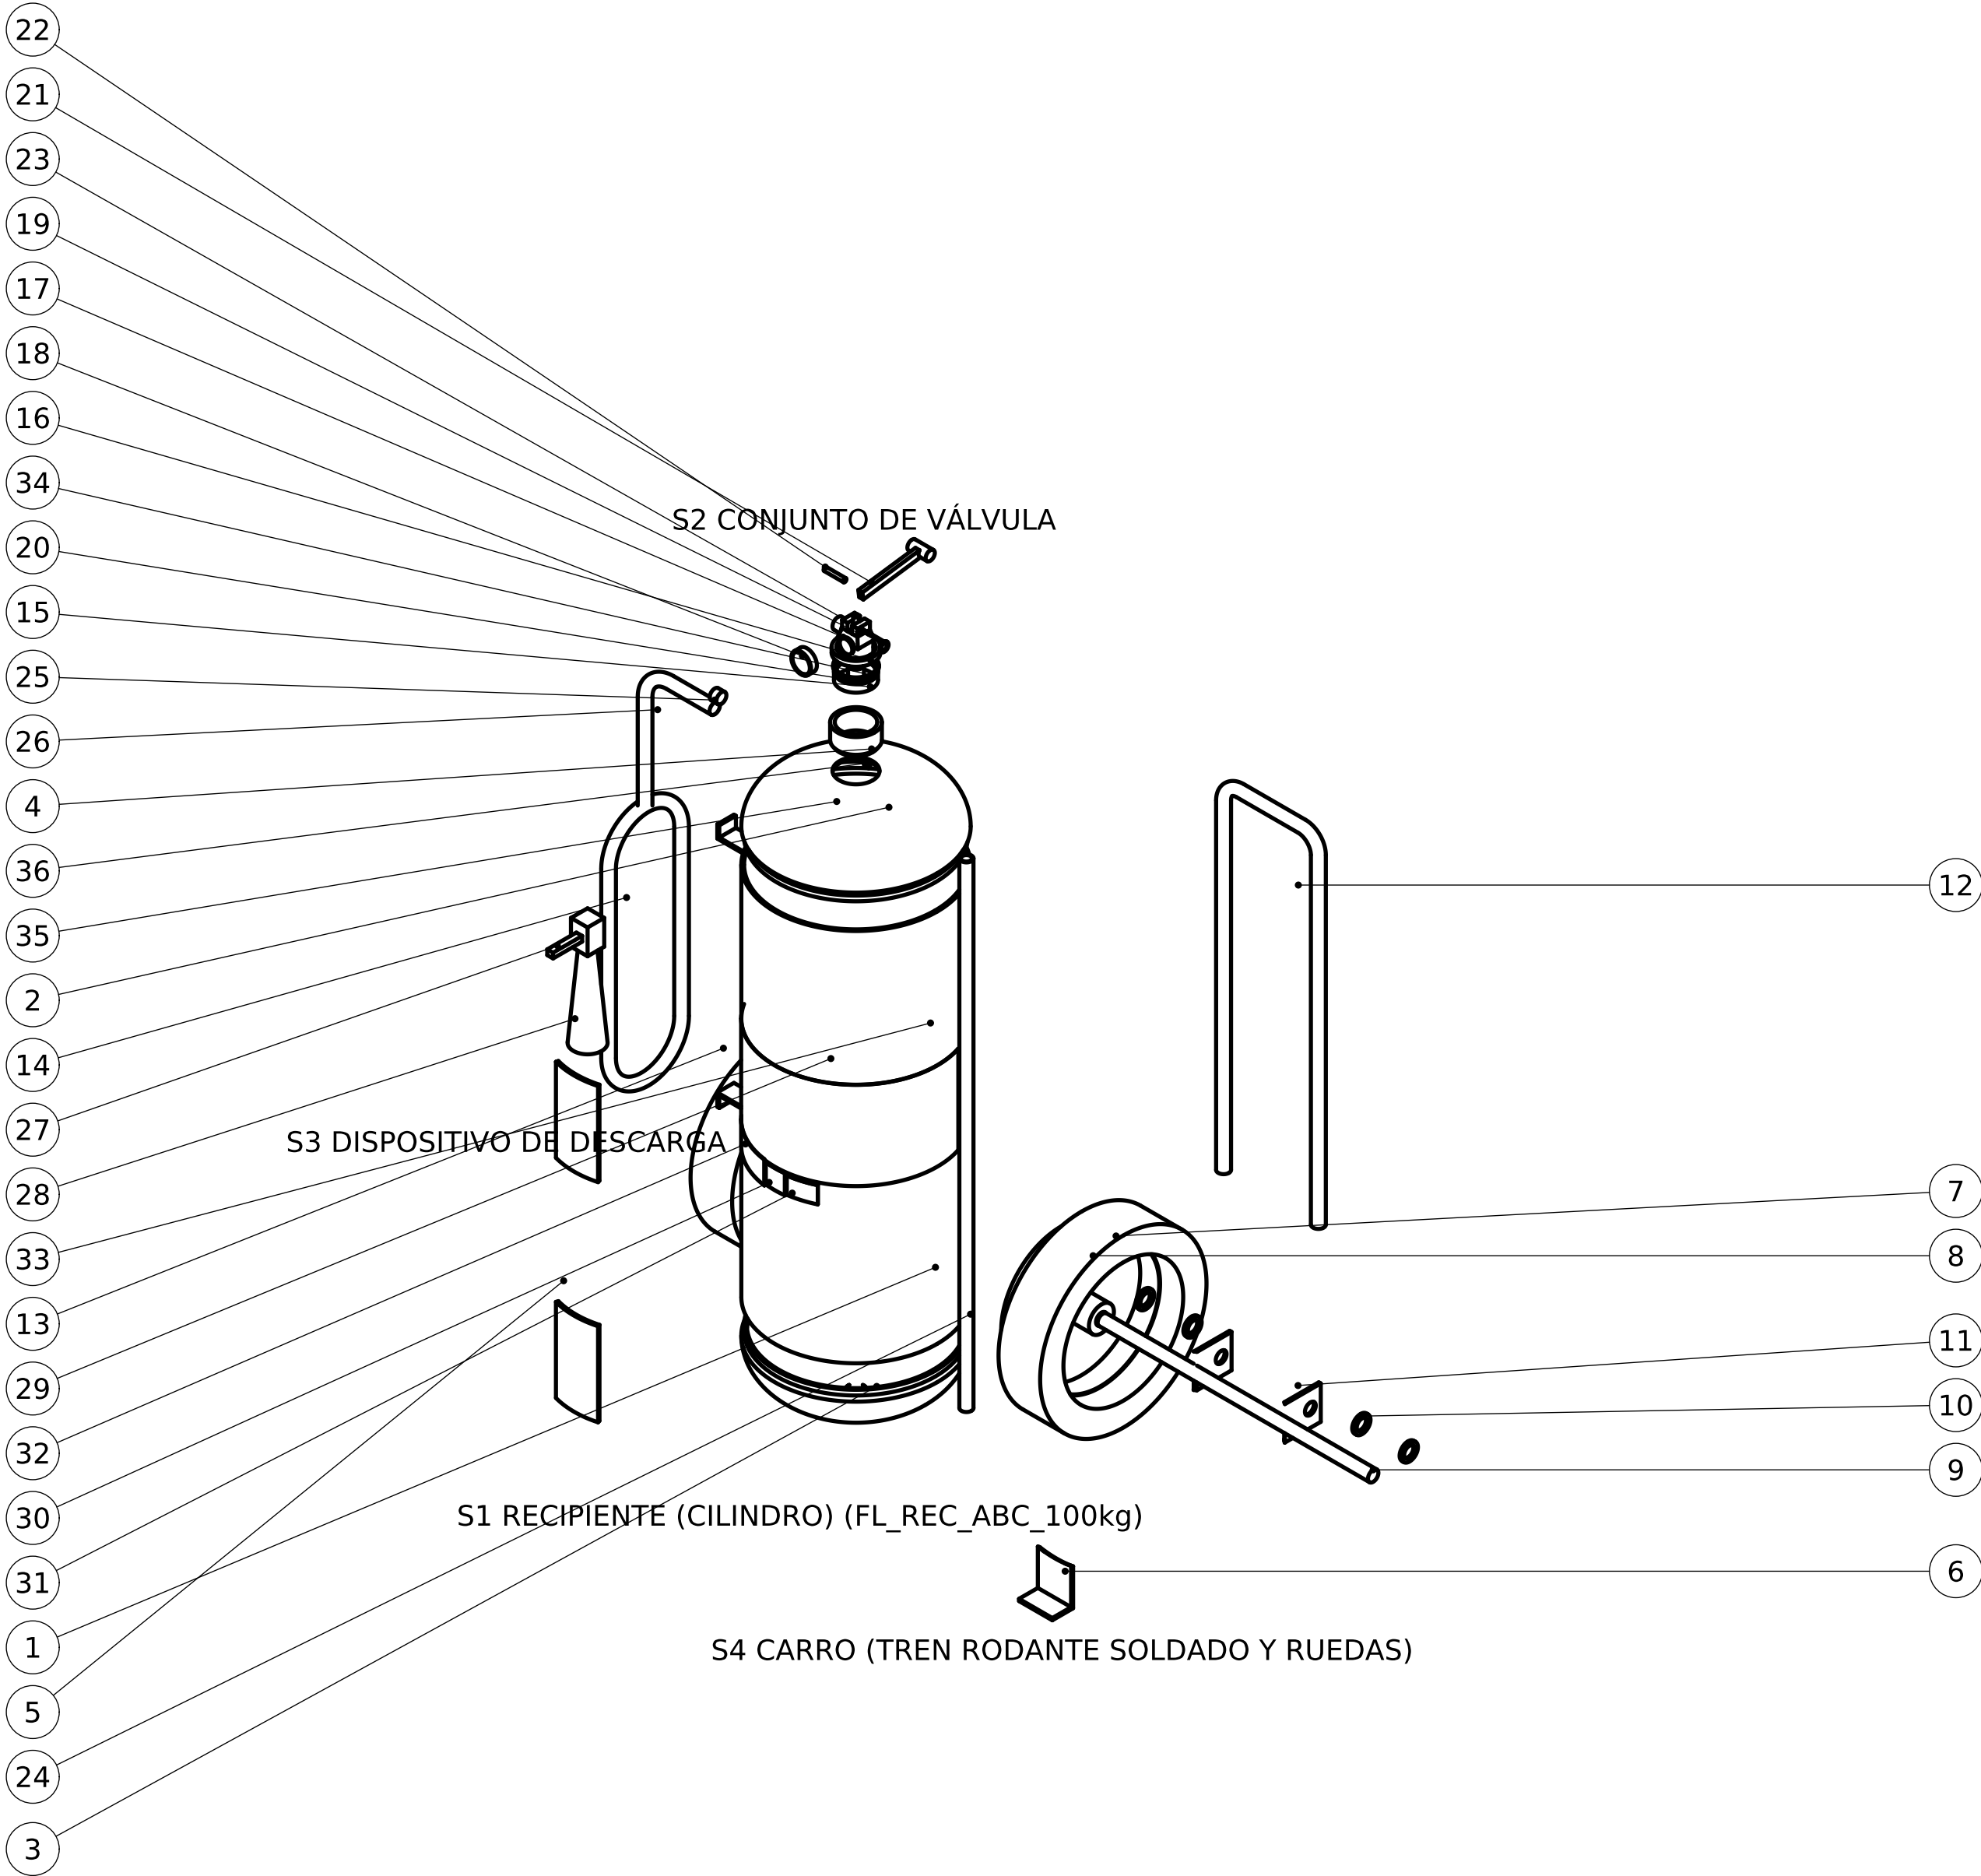

LISTA DE DESPIECE - BOM FL_MAT ABC 100kg				
Glo.	Código BOM	Denominación	Cant.	Material
	FL_REC_ABC_100kg	RECIPIENTE (CILINDRO)		
1	ABC100-01	Cuerpo (virola)	1	Chapa LAC IRAM-IAS U 500-04 e=4,75
2	ABC100-02	Cúpula	1	Chapa LAC IRAM-IAS U 500-04 e=4,75
3	ABC100-03	Fondo	1	Chapa LAC IRAM-IAS U 500-04 e=4,75
4	ABC100-04	Cuello roscado	1	Acero SAE 1010
5	ABC100-05	Placas de refuerzo (2)	1	Chapa LAC 4,75 curvada a Ø380
—	ABC100-C1	Alambre MAG ER70S-6 Ø1,2 (AWS A5.18)	1,0956 kg	ER70S-6
—	ABC100-C2	Gas de protección MAG Arcal 21 / ARCAL Speed (Ar + 8 % CO ₂ , M20)	84,6 L	EN ISO 14175 M20-Arc-8
—	ABC100-C4	Servicio de pintura en polvo al horno 03-1-050 (con preparación por quemado)	1	Servicio tercerizado
	ABC100-S2	CONJUNTO DE VÁLVULA		
15	ABC100-15	Espiga roscada	1	Latón forjado
16	ABC100-16	Collarín de válvula	1	Latón forjado
17	ABC100-17	Cuerpo de válvula	1	Latón forjado
18	ABC100-18	Manómetro	1	Comercial
19	ABC100-19	Vástago	1	Latón
20	ABC100-20	Resorte de válvula	1	Alambre acero inox. AISI 302
21	ABC100-21	Palanca de accionamiento	1	Planchuela acero SAE 1010 10 x 16 pintada
22	ABC100-22	Eje de palanca	1	Acero inox. AISI 304
23	ABC100-23	Pasador de seguridad	1	Alambre acero inox. AISI 304
24	ABC100-24	Caño de pesca (sifón)	1	Tubo PVC rígido
34	ABC100-34	Junta tórica de asiento	1	NBR 70 Shore A
—	ABC100-K2	Válvula HZ armada de carro 50-70-100 kg	1	Latón forjado (HZ)
—	ABC100-V2	Resorte de retorno del vástago	1	Acero para resortes
—	ABC100-V3	Junta tórica del vástago	1	NBR 70 Shore A
	ABC100-S3	DISPOSITIVO DE DESCARGA		
14	ABC100-14	Manguera (tramo enrollado)	1	Caucho sintético
25	ABC100-25	Racor de manguera	1	Latón
26	ABC100-26	Manguera	1	Caucho sintético
27	ABC100-27	Válvula esférica	1	Latón cromado
28	ABC100-28	Tobera campana	1	Polipropileno
	ABC100-S4	CARRO (TREN RODANTE SOLDADO Y RUEDAS)		
6	ABC100-06	Tercera pata	1	Chapa LAC del cuerpo (orilla) plegada
7	ABC100-07	Rueda con cubierta neumática	2	Caucho
8	ABC100-08	Llanta con cubo	2	Chapa acero SAE 1010
9	ABC100-09	Eje de ruedas	1	Barra acero SAE 1045 Ø25
10	ABC100-10	Arandelas de tope (4)	1	Acero SAE 1010 Ø40 x Ø26 x 4
11	ABC100-11	Soportes del eje (2)	1	Chapa LAC del cuerpo (orilla)
12	ABC100-12	Manija del carro	1	Caño acero SAE 1010 Ø25,4x1,6
13	ABC100-13	Ganchos portamanguera (2)	1	Chapa LAC del cuerpo (orilla) plegada
	ABC100-S5	CARGA: AGENTE EXTINTOR Y GAS IMPULSOR		
—	ABC100-A1	Polvo químico seco ABC 90 (Sello IRAM 3569)	100 kg	Polvo químico seco ABC 90 (Sello IRAM 3569)
—	ABC100-A2	Gas impulsor: N ₂	0,5189 kg	N ₂
	ABC100-S6	IDENTIFICACIÓN Y PRECINTO		
29	ABC100-29	Etiqueta / placa de características	1	Vinilo autoadhesivo laminado
30	ABC100-30	Oblea de fabricación (PBA)	1	Papel de seguridad autodestructible
31	ABC100-31	Estampilla IRAM de conformidad	1	Provista por IRAM (Anexo R)
32	ABC100-32	Tarjeta de identificación AGC (CABA)	1	Etiqueta autoadhesiva emitida por la AGC
33	ABC100-33	Etiqueta de n° de serie GS1	1	Poliéster autoadhesivo impreso térmico
35	ABC100-35	Faja de garantía válvula-cuello	1	Vinilo destructible rayado rojo/blanco
36	ABC100-36	Precinto de fábrica	1	Polipropileno color
	ABC100-S7	EMBALAJE		
—	ABC100-E1	Esquineros y funda de polietileno	1 jgo	PE / cartón
—	ABC100-E3	Pallet 1200 x 1000 (fracción)	1	Madera
—	ABC100-E4	Film stretch (fracción del pallet)	0,12 kg	PE lineal 23 µm
—	ABC100-E5	Etiqueta de pallet (lote y destino, fracción)	1	Papel térmico

NOTAS

- Lista completa con medidas, pesos, origen, operación y norma: salida/bom/FLAMA_BOM.xlsx, hoja BOM_FL_MAT_ABC_100kg.
- «—» = ítem no dibujado (internos de válvula, carga, identificación, embalaje).
- S1 en los ABC = recipiente FL_REC (mismo plano que el cilindro de venta suelta).
- Ruedas: se dibujan ambas, el globo señala la derecha (cantidad 2).

	Fecha	Nombre	Propietario FLAMA S.A.		Reemplaza a / Reemplazado por -	
Dibujó	28/09/26	T. Sinay			Material	
Revisó			Denominación Despiece ABC 100 kg sobre ruedas Vista explosionada y lista multinivel (BOM)		Ver lista	
Aprobó					Edición 0	
Escala 1:10		Método de proyección  ISO E		Hoja 1 / 1		Idioma es
Tolerancias generales ISO 2768-m		Formato A2		N° de plano FL_DES_ABC_100kg		