

A

B

C

D

E


F

G

H

DESPIECE - EXTINTOR ABC 100 KG SOBRE RUEDAS

Isometría explosionada por subconjunto, escala 1:10. Globo = posición del plano FL_MAT_ABC_100kg = código ABC100-NN

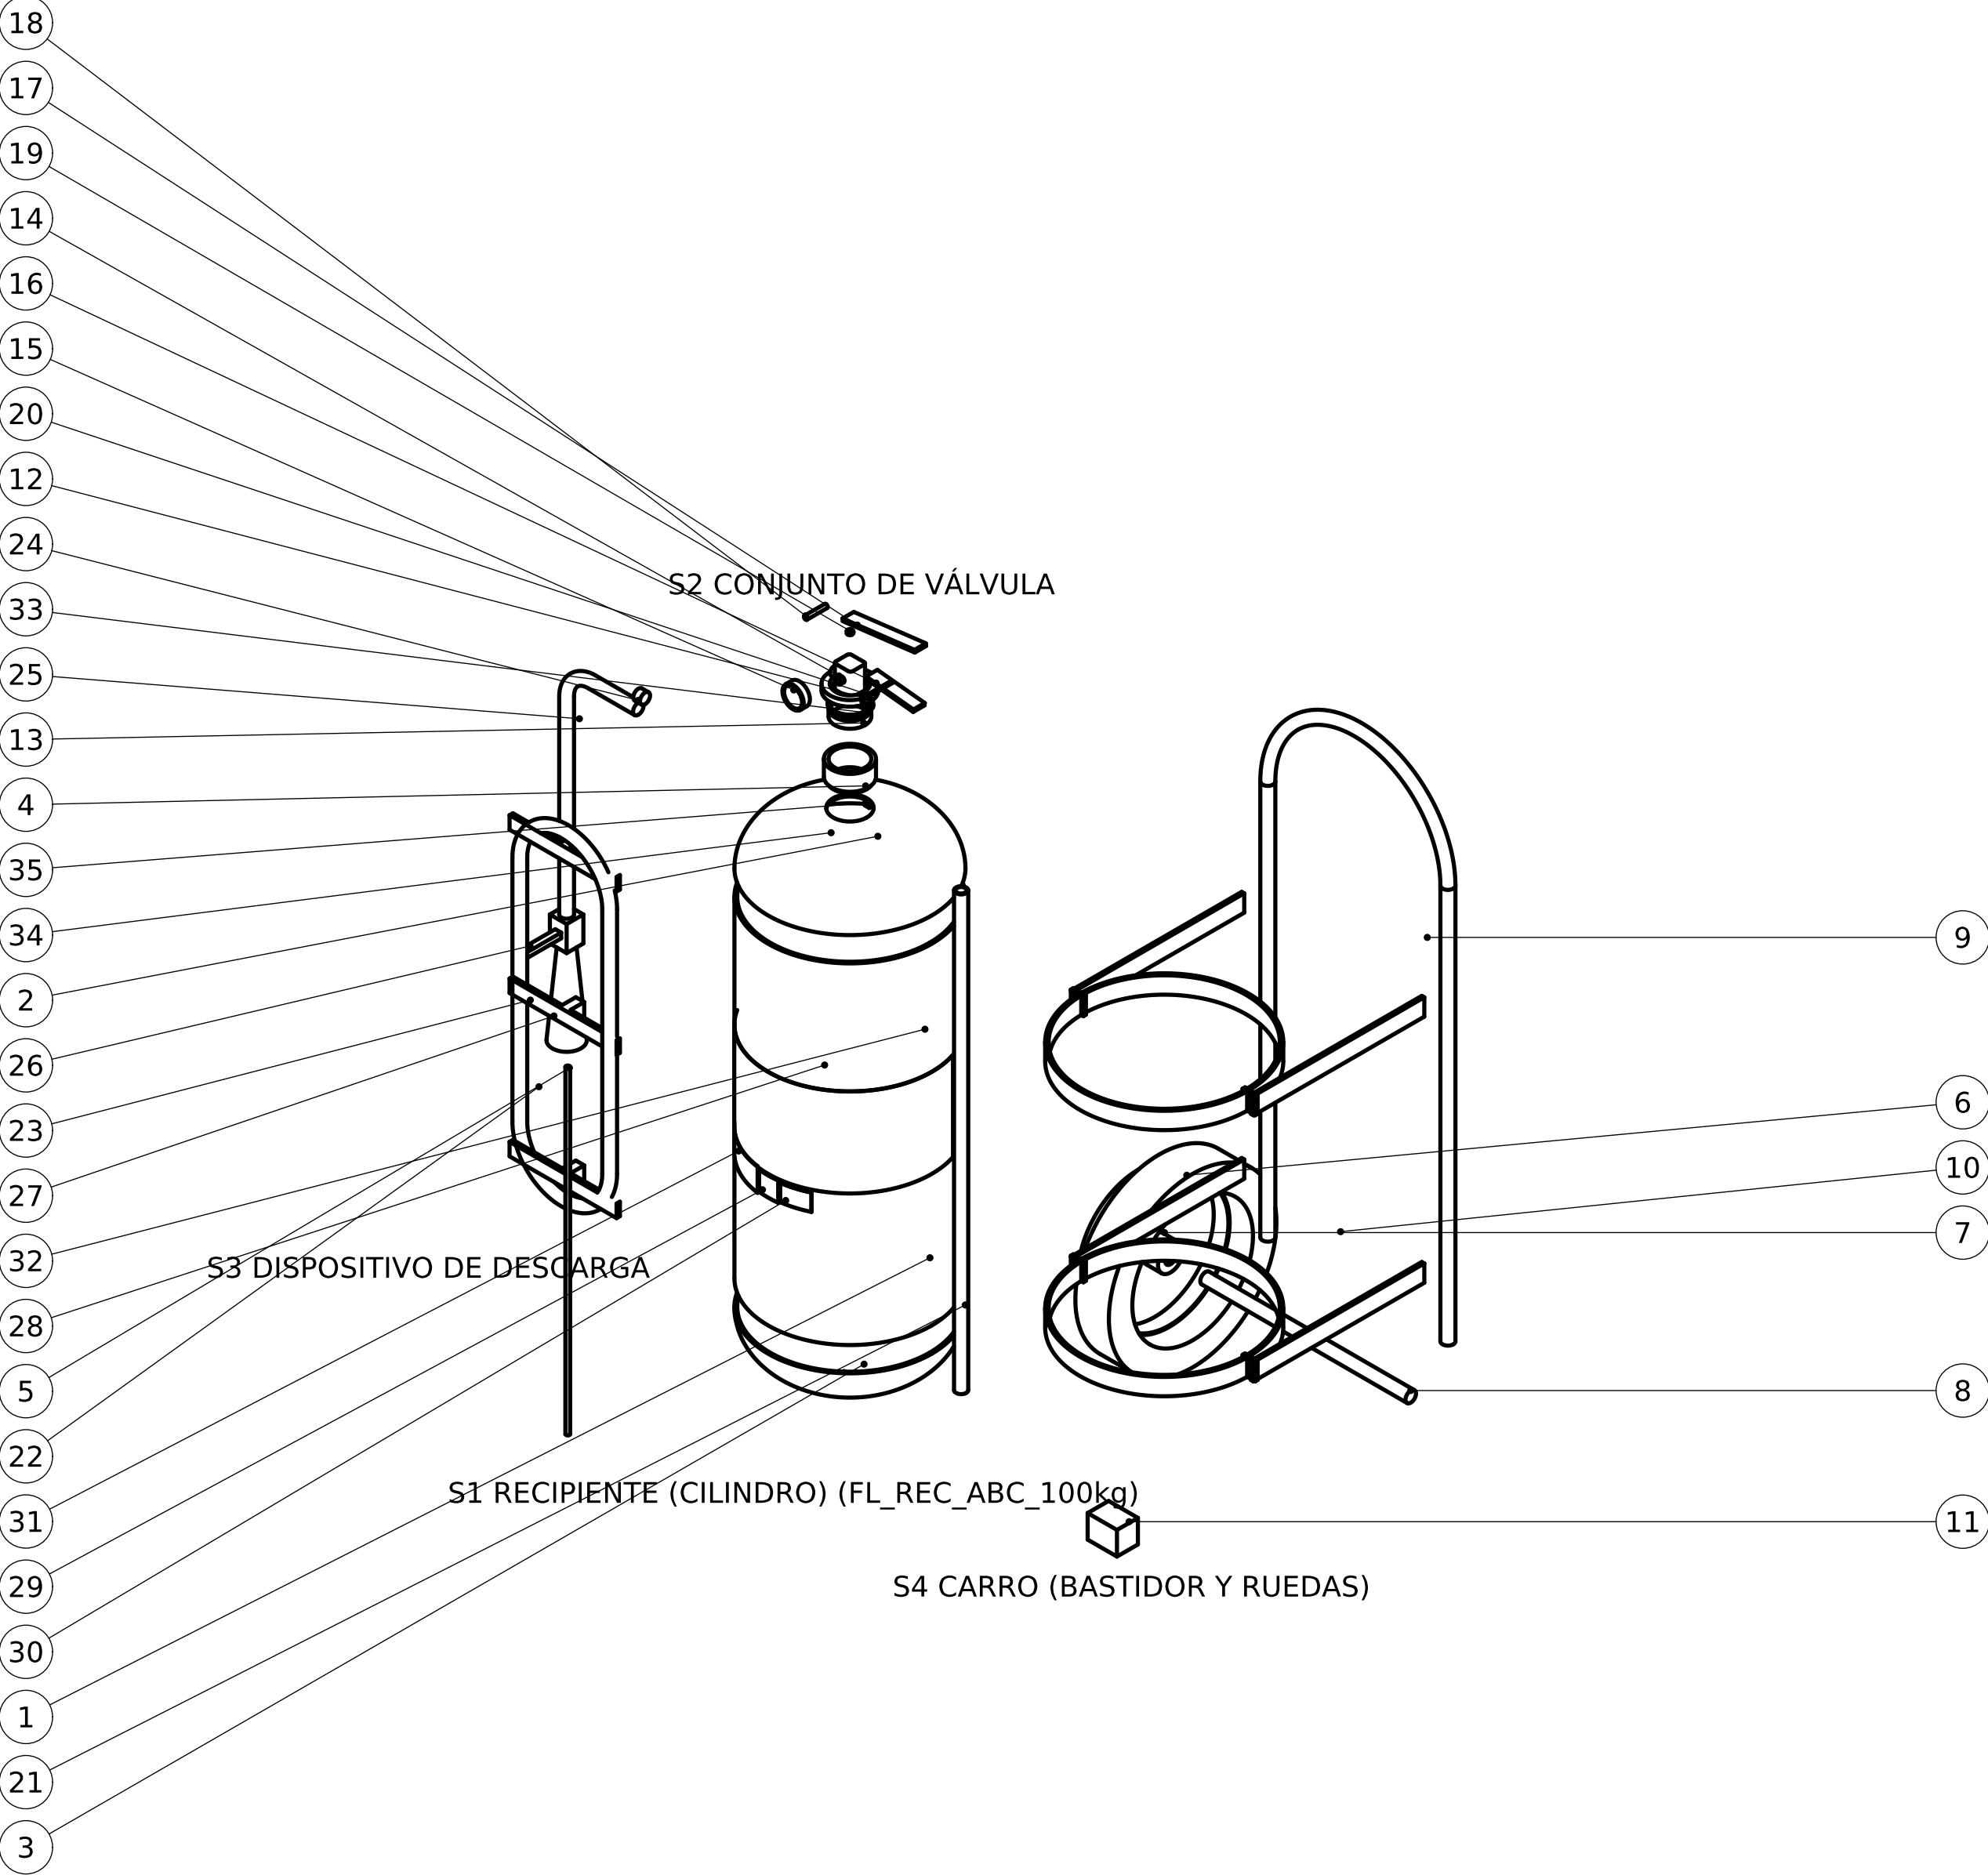

LISTA DE DESPIECE - BOM FL_MAT ABC 100kg

Glo.	Código BOM	Denominación	Cant.	Material
	FL_REC_ABC_100kg	RECIPIENTE (CILINDRO)		
1	ABC100-01	Cuerpo (virola)	1	Chapa LAC IRAM-IAS U 500-04 e=
2	ABC100-02	Cúpula	1	Chapa LAC IRAM-IAS U 500-04 e=
3	ABC100-03	Fondo	1	Chapa LAC IRAM-IAS U 500-04 e=
4	ABC100-04	Cuello roscado	1	Acero SAE 1010
5	ABC100-05	Varilla de refuerzo interior	1	Redondo liso SAE 1010 Ø8
—	ABC100-C1	Alambre MAG ER70S-6 Ø1,2 (AWS A5.18)	1,0848 kg	ER70S-6
—	ABC100-C2	Gas de protección MAG Arcal 21 / ARCAL Speed (	82 L	EN ISO 14175 M20-Arc-8
—	ABC100-C4	Servicio de pintura en polvo al horno, rojo 03	1	Servicio tercerizado
	ABC100-S2	CONJUNTO DE VÁLVULA		
12	ABC100-12	Collarín de válvula	1	Latón forjado
13	ABC100-13	Espiga roscada	1	Latón forjado
14	ABC100-14	Cuerpo de válvula	1	Latón forjado
15	ABC100-15	Manómetro	1	Comercial
16	ABC100-16	Manija de transporte	1	Chapa acero SAE 1010 pintada
17	ABC100-17	Manija de accionamiento	1	Chapa acero SAE 1010 pintada
18	ABC100-18	Eje de palanca	1	Acero inox. AISI 304
19	ABC100-19	Vástago	1	Latón
20	ABC100-20	Pasador de seguridad	1	Alambre acero inox. AISI 304
21	ABC100-21	Caño de pesca (sifón)	1	Tubo PVC rígido
33	ABC100-33	Junta tórica de asiento	1	NBR 70 Shore A
—	ABC100-K2	Válvula HZ armada de carro 50-70-100 kg	1	Latón forjado (HZ)
—	ABC100-V2	Resorte de retorno del vástago	1	Acero para resortes
—	ABC100-V3	Junta tórica del vástago	1	NBR 70 Shore A
	ABC100-S3	DISPOSITIVO DE DESCARGA		
22	ABC100-22	Manguera (tramo enrollado)	1	Caucho sintético
23	ABC100-23	Soporte de manguera	1	Planchuela acero SAE 1010
24	ABC100-24	Racor de manguera	1	Latón
25	ABC100-25	Manguera	1	Caucho sintético
26	ABC100-26	Válvula esférica	1	Latón cromado
27	ABC100-27	Tobera campana	1	Polipropileno
	ABC100-S4	CARRO (BASTIDOR Y RUEDAS)		
6	ABC100-06	Neumático macizo	2	Caucho
7	ABC100-07	Llanta con cubo	2	Chapa acero SAE 1010
8	ABC100-08	Eje de ruedas	1	Acero SAE 1045
9	ABC100-09	Bastidor	1	Caño acero SAE 1010 Ø25,4×1,6
10	ABC100-10	Sunchos de fijación	1	Planchuela acero SAE 1010
11	ABC100-11	Apoyo delantero	1	Chapa acero SAE 1010 plegada
	ABC100-S5	CARGA: AGENTE EXTINTOR Y GAS IMPULSOR		
—	ABC100-A1	Polvo químico seco ABC 90 (Sello IRAM 3569)	100 kg	Polvo químico seco ABC 90 (Sel
—	ABC100-A2	Gas impulsor: N ₂	0,5534 kg	N ₂
	ABC100-S6	IDENTIFICACIÓN Y PRECINTO		
28	ABC100-28	Etiqueta / placa de características	1	Vinilo autoadhesivo laminado
29	ABC100-29	Oblea de fabricación (PBA)	1	Papel de seguridad autodestruc
30	ABC100-30	Estampilla IRAM de conformidad	1	Provista por IRAM (Anexo R)
31	ABC100-31	Tarjeta de identificación AGC (CABA)	1	Etiqueta autoadhesiva emitida
32	ABC100-32	Etiqueta de n° de serie GS1	1	Poliéster autoadhesivo impreso
34	ABC100-34	Faja de garantía válvula-cuello	1	Vinilo destructible rayado roj
35	ABC100-35	Precinto de fábrica	1	Polipropileno color
	ABC100-S7	EMBALAJE		
—	ABC100-E1	Esquineros y funda de polietileno	1 jgo	PE / cartón
—	ABC100-E3	Pallet 1200 × 1000 (fracción)	1	Madera
—	ABC100-E4	Film stretch (fracción del pallet)	0,12 kg	PE lineal 23 µm
—	ABC100-E5	Etiqueta de pallet (lote y destino, fracción)	1	Papel térmico

NOTAS

- Lista completa con medidas, pesos, origen, operación y norma: salida/bom/FLAMA_BOM.xlsx, hoja BOM_FL_MAT_ABC_100kg.
- «—» = ítem no dibujado (internos de válvula, carga, identificación, embalaje).
- S1 en los ABC = recipiente FL_REC (mismo plano que el cilindro de venta suelta).
- Ruedas: se dibujan ambas, el globo señala la derecha (cantidad 2).

	Fecha	Nombre	Propietario FLAMA S.A.		Reemplaza a / Reemplazado por	
Dibujó	28/09/26	T. Sinay			-	
Revisó			Denominación Despiece ABC 100 kg sobre ruedas		Material	
Aprobó					Ver lista	
Escala	Método de proyección		Vista explosionada y lista multinivel (BOM)		Edición	Fecha de emisión
1:10	 ISO E				0	28/09/2026
Tolerancias generales		Formato	Tipo de documento Plano de despiece		Hoja	Idioma
ISO 2768-m		A2			1 / 1	es
					N° de plano	
					FL_DES_ABC_100kg	