

A

B

C

D

E


F

G

H

DESPIECE - EXTINTOR ABC 25 KG SOBRE RUEDAS

Isometría explosionada por subconjunto, escala 1:5. Globo = posición del plano FL_MAT_ABC_25kg = código ABC25-NN

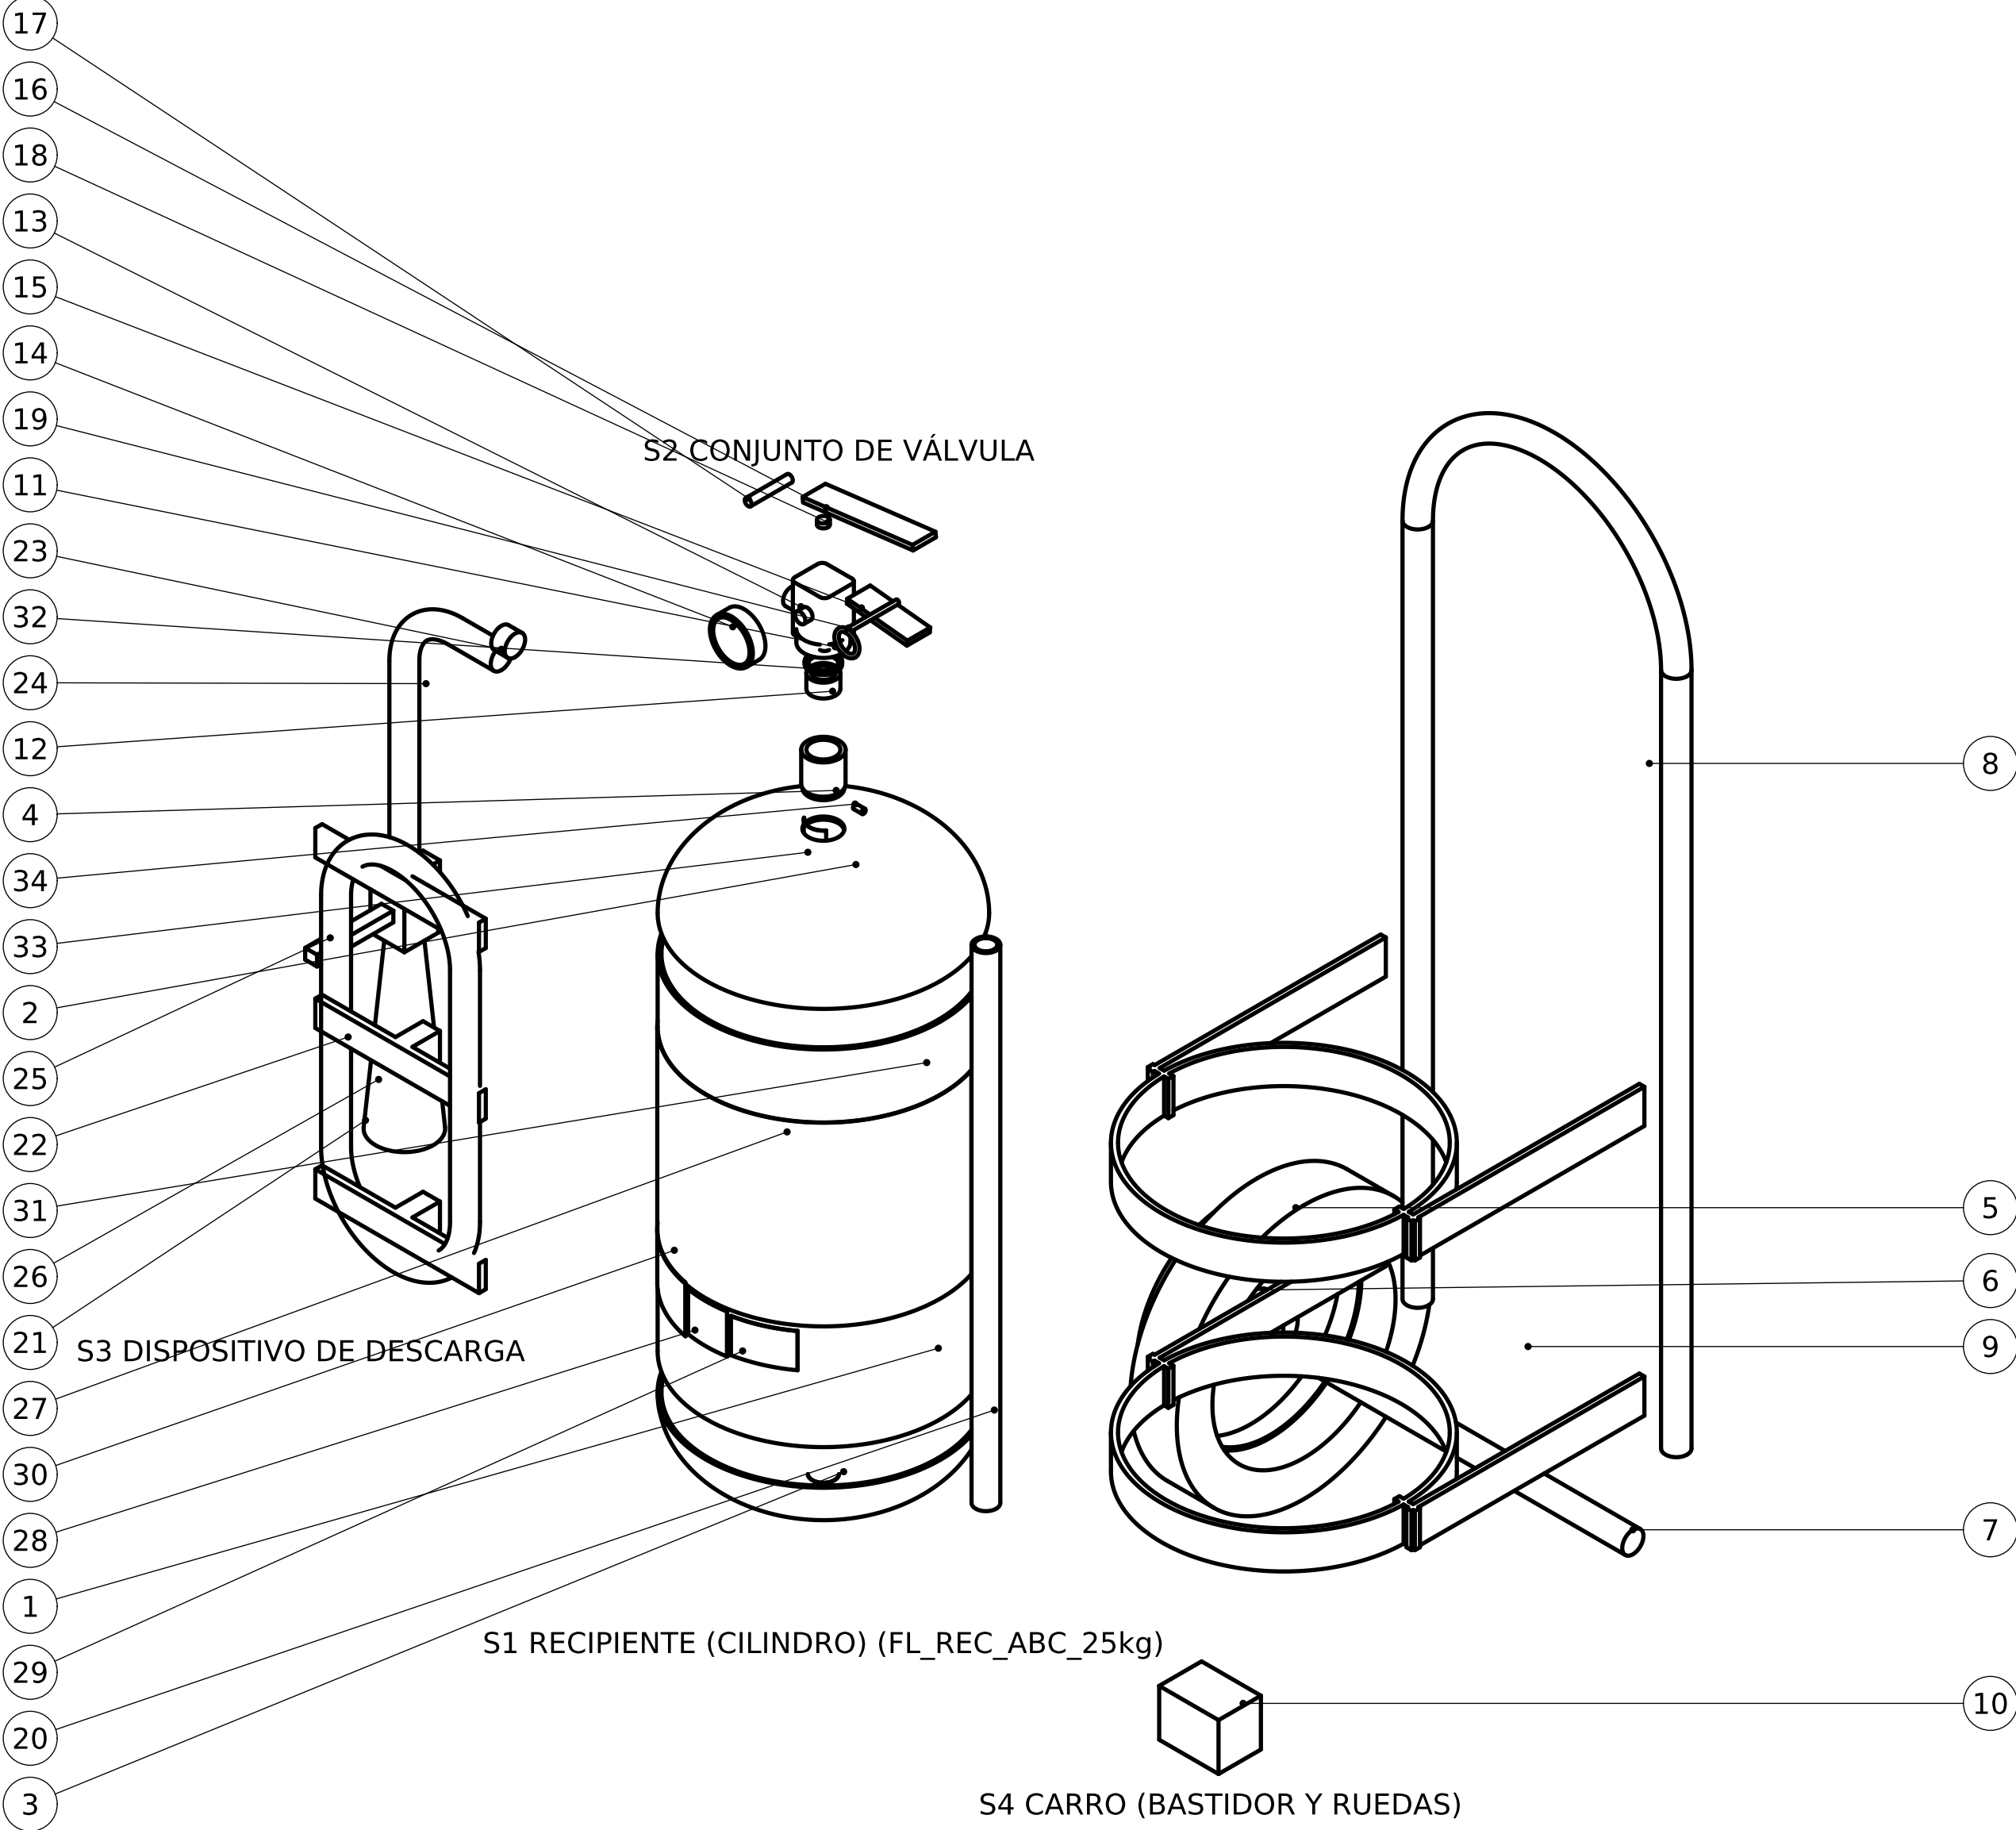

LISTA DE DESPIECE - BOM FL_MAT_ABC_25kg				
Glo.	Código BOM	Denominación	Cant.	Material
	FL_REC_ABC_25kg	RECIPIENTE (CILINDRO)		
1	ABC25-01	Cuerpo (virola)	1	Chapa LAC IRAM-IAS U 500-04 e=
2	ABC25-02	Cúpula	1	Chapa LAC IRAM-IAS U 500-04 e=
3	ABC25-03	Fondo	1	Chapa LAC IRAM-IAS U 500-04 e=
4	ABC25-04	Cuello roscado	1	Acero SAE 1010
—	ABC25-C1	Alambre MAG ER70S-6 Ø1,2 (AWS A5.18)	0,3374 kg	ER70S-6
—	ABC25-C2	Gas de protección MAG Arcal 21 / ARCAL Speed (	52,7 L	EN ISO 14175 M20-Arc-8
—	ABC25-C4	Servicio de pintura en polvo al horno, rojo 03	1	Servicio tercerizado
	ABC25-S2	CONJUNTO DE VÁLVULA		
11	ABC25-11	Collarín de válvula	1	Latón forjado
12	ABC25-12	Espiga roscada	1	Latón forjado
13	ABC25-13	Cuerpo de válvula	1	Latón forjado
14	ABC25-14	Manómetro	1	Comercial
15	ABC25-15	Manija de transporte	1	Chapa acero SAE 1010 pintada
16	ABC25-16	Manija de accionamiento	1	Chapa acero SAE 1010 pintada
17	ABC25-17	Eje de palanca	1	Acero inox. AISI 304
18	ABC25-18	Vástago	1	Latón
19	ABC25-19	Pasador de seguridad	1	Alambre acero inox. AISI 304
20	ABC25-20	Caño de pesca (sifón)	1	Tubo PVC rígido
32	ABC25-32	Junta tórica de asiento	1	NBR 70 Shore A
—	ABC25-K2	Válvula HZ armada de carro 25 kg c/traba, mani	1	Latón forjado (HZ)
—	ABC25-V2	Resorte de retorno del vástago	1	Acero para resortes
—	ABC25-V3	Junta tórica del vástago	1	NBR 70 Shore A
	ABC25-S3	DISPOSITIVO DE DESCARGA		
21	ABC25-21	Manguera (tramo enrollado)	1	Caucho sintético
22	ABC25-22	Soporte de manguera	1	Planchuela acero SAE 1010
23	ABC25-23	Racor de manguera	1	Latón
24	ABC25-24	Manguera	1	Caucho sintético
25	ABC25-25	Válvula esférica	1	Latón cromado
26	ABC25-26	Tobera campana	1	Polipropileno
	ABC25-S4	CARRO (BASTIDOR Y RUEDAS)		
5	ABC25-05	Neumático macizo	2	Caucho
6	ABC25-06	Llanta con cubo	2	Chapa acero SAE 1010
7	ABC25-07	Eje de ruedas	1	Acero SAE 1045
8	ABC25-08	Bastidor	1	Caño acero SAE 1010 Ø25,4x1,6
9	ABC25-09	Sunchos de fijación	1	Planchuela acero SAE 1010
10	ABC25-10	Apoyo delantero	1	Chapa acero SAE 1010 plegada
	ABC25-S5	CARGA: AGENTE EXTINTOR Y GAS IMPULSOR		
—	ABC25-A1	Polvo químico seco ABC 90 (Sello IRAM 3569)	25 kg	Polvo químico seco ABC 90 (Sel
—	ABC25-A2	Gas impulsor: N ₂	0,2013 kg	N ₂
	ABC25-S6	IDENTIFICACIÓN Y PRECINTO		
27	ABC25-27	Etiqueta / placa de características	1	Vinilo autoadhesivo laminado
28	ABC25-28	Oblea de fabricación (PBA)	1	Papel de seguridad autodestruc
29	ABC25-29	Estampilla IRAM de conformidad	1	Provista por IRAM (Anexo R)
30	ABC25-30	Tarjeta de identificación AGC (CABA)	1	Etiqueta autoadhesiva emitida
31	ABC25-31	Etiqueta de n° de serie GS1	1	Poliéster autoadhesivo impreso
33	ABC25-33	Faja de garantía válvula-cuello	1	Vinilo destructible rayado roj
34	ABC25-34	Precinto de fábrica	1	Polipropileno color
	ABC25-S7	EMBALAJE		
—	ABC25-E1	Esquineros y funda de polietileno	1 jgo	PE / cartón
—	ABC25-E3	Pallet 1200 x 1000 (fracción)	0,5	Madera
—	ABC25-E4	Film stretch (fracción del pallet)	0,06 kg	PE lineal 23 µm
—	ABC25-E5	Etiqueta de pallet (lote y destino, fracción)	0,5	Papel térmico

NOTAS

1) Lista completa con medidas, pesos, origen, operación y norma: salida/bom/FLAMA_BOM.xlsx, hoja BOM_FL_MAT_ABC_25kg.

2) «—» = ítem no dibujado (internos de válvula, carga, identificación, embalaje).

3) S1 en los ABC = recipiente FL_REC (mismo plano que el cilindro de venta suelta).

4) Ruedas: se dibujan ambas, el globo señala la derecha (cantidad 2).

	Fecha	Nombre	Propietario FLAMA S.A.		Reemplaza a / Reemplazado por -	
Dibujó	28/09/26	T. Sinay			Material	
Revisó			Denominación Despiece ABC 25 kg sobre ruedas Vista explosionada y lista multinivel (BOM)		Ver lista	
Aprobó					Edición	
Escala 1:5		Método de proyección  ISO E		0		28/09/2026
Tolerancias generales ISO 2768-m		Formato A2		Hoja 1 / 1		Idioma es
Tipo de documento Plano de despiece				N° de plano FL_DES_ABC_25kg		