


DESPIECE - EXTINTOR AFFF 50 L SOBRE RUEDAS

Isometría explosionada por subconjunto, escala 1:5. Globo = posición del plano FL_MAT_AFFF_50l = código AFFF50-NN

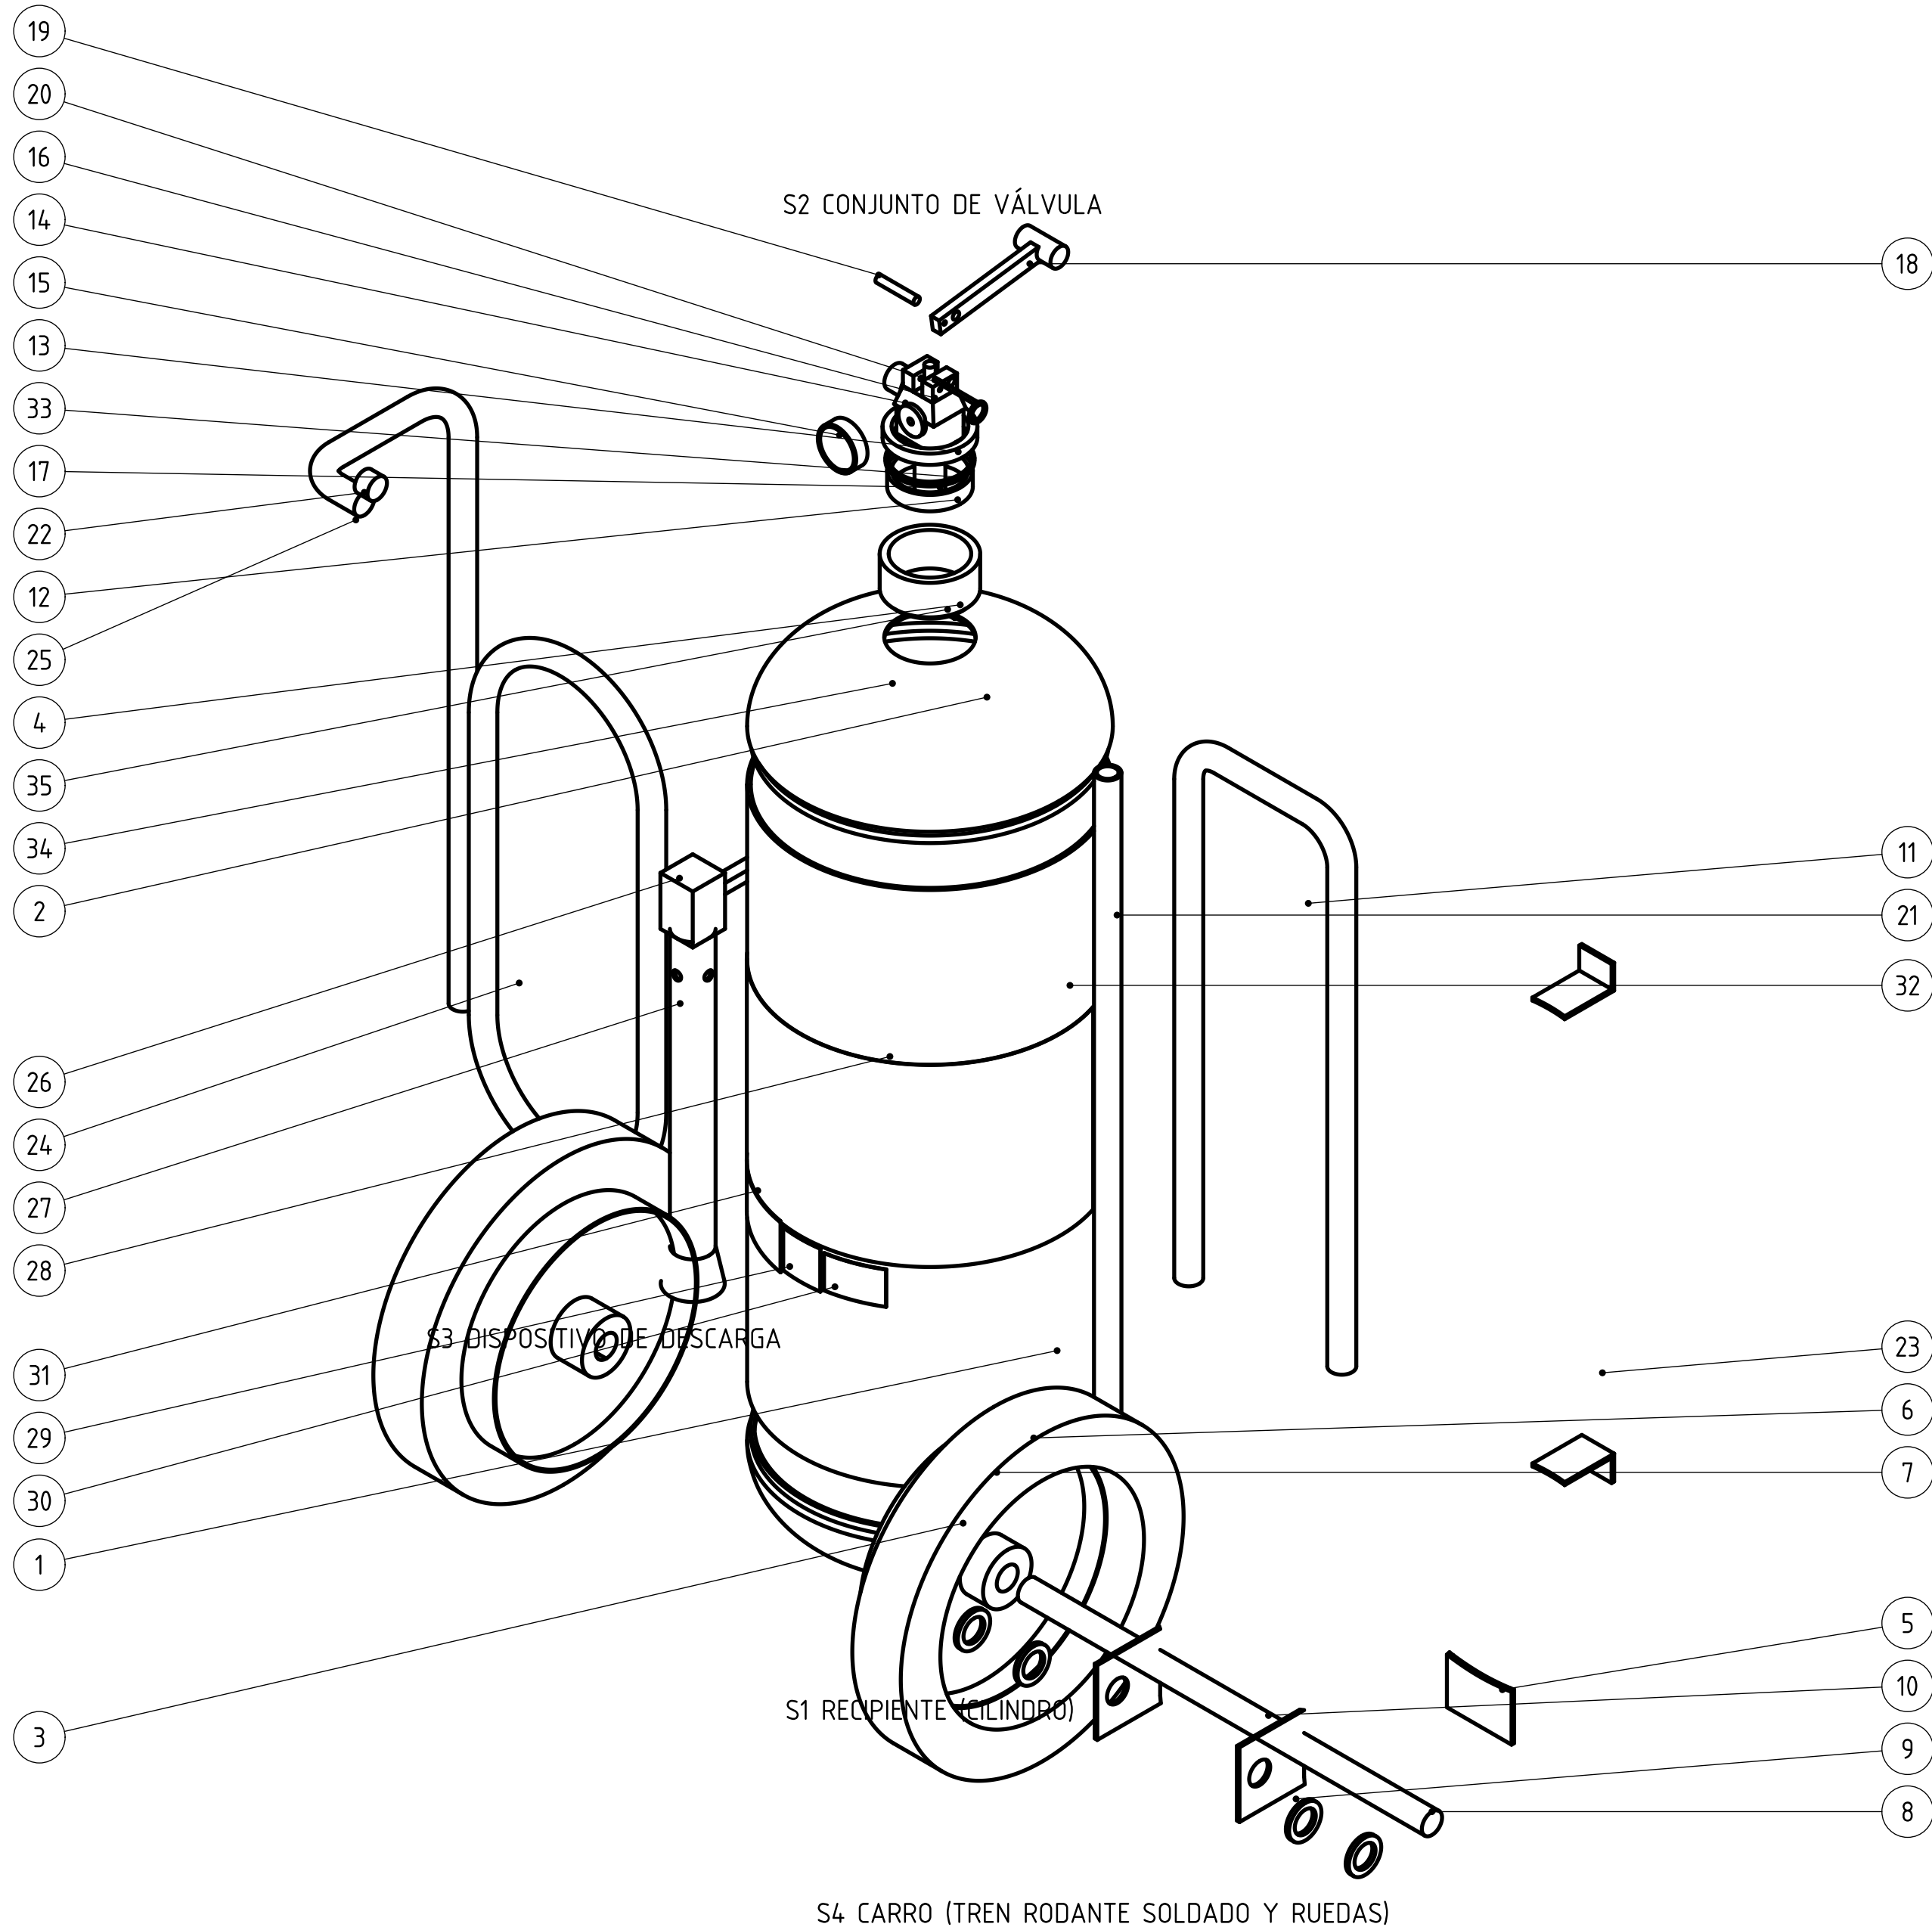

LISTA DE DESPIECE - BOM FL_MAT_AFFF_50l				
Glo.	Código BOM	Denominación	Cant.	Material
	AFFF50-S0	EQUIPO TERMINADO COMPRADO (FABRICANTE CON SELLO IRAM)		
	AFFF50-S1	RECIPIENTE (CILINDRO)		
1	AFFF50-01	Cuerpo (virola)	1	Chapa LAC IRAM-IAS U 500-04 e=3,2
2	AFFF50-02	Cúpula	1	Chapa LAC IRAM-IAS U 500-04 e=3,2
3	AFFF50-03	Fondo	1	Chapa LAC IRAM-IAS U 500-04 e=3,2
4	AFFF50-04	Cuello roscado	1	Acero SAE 1010
	AFFF50-S2	CONJUNTO DE VÁLVULA		
12	AFFF50-12	Espiga roscada	1	Latón forjado
13	AFFF50-13	Collarín de válvula	1	Latón forjado
14	AFFF50-14	Cuerpo de válvula	1	Latón forjado
15	AFFF50-15	Manómetro	1	Comercial
16	AFFF50-16	Vástago	1	Latón
17	AFFF50-17	Resorte de válvula	1	Alambre acero inox. AISI 302
18	AFFF50-18	Palanca de accionamiento	1	Planchuela acero SAE 1010 10 x 16 pintada
19	AFFF50-19	Eje de palanca	1	Acero inox. AISI 304
20	AFFF50-20	Pasador de seguridad	1	Alambre acero inox. AISI 304
21	AFFF50-21	Caño de pesca (sifón)	1	Tubo PVC rígido
33	AFFF50-33	Junta tórica de asiento	1	NBR 70 Shore A
—	AFFF50-V2	Resorte de retorno del vástago	1	Acero para resortes
—	AFFF50-V3	Junta tórica del vástago	1	NBR 70 Shore A
	AFFF50-S3	DISPOSITIVO DE DESCARGA		
22	AFFF50-22	Racor de manguera	1	Latón
24	AFFF50-24	Manguera (tramo enrollado)	1	Caucho sintético
25	AFFF50-25	Manguera	1	Caucho sintético
26	AFFF50-26	Válvula esférica	1	Latón cromado
27	AFFF50-27	Lanza espumígena	1	Polipropileno
	AFFF50-S4	CARRO (TREN RODANTE SOLDADO Y RUEDAS)		
5	AFFF50-05	Tercera pata	1	Chapa LAC 3.2 (orilla de la hoja de 25 kg)
6	AFFF50-06	Neumático macizo	2	Caucho
7	AFFF50-07	Llanta con cubo	2	Chapa acero SAE 1010
8	AFFF50-08	Eje de ruedas	1	Barra acero SAE 1045 Ø25
9	AFFF50-09	Arandelas de tope (4)	1	Acero SAE 1010 Ø40 x Ø26 x 4
10	AFFF50-10	Soportes del eje (2)	1	Chapa LAC del cuerpo (orilla)
11	AFFF50-11	Manija del carro	1	Caño acero SAE 1010 Ø25,4x1,6
23	AFFF50-23	Ganchos portamanguera (2)	1	Chapa LAC del cuerpo (orilla) plegada
	AFFF50-S5	CARGA: AGENTE EXTINTOR Y GAS IMPULSOR		
—	AFFF50-A1	Agua potable (premezcla)	48,5 L	Agua
—	AFFF50-A1b	Concentrado espumígeno AFFF 3 % (IRAM 3515)	1,5 L	Concentrado espumígeno AFFF 3 % (IRAM 3515)
—	AFFF50-A2	Gas impulsor: Aire comprimido	0,1265 kg	Aire comprimido
	AFFF50-S6	IDENTIFICACIÓN Y PRECINTO		
28	AFFF50-28	Etiqueta / placa de características	1	Vinito autoadhesivo laminado
29	AFFF50-29	Oblea de fabricación (PBA)	1	Papel de seguridad autodestructible
30	AFFF50-30	Estampilla IRAM de conformidad	1	Provista por IRAM (Anexo R)
31	AFFF50-31	Tarjeta de identificación AGC (CABA)	1	Etiqueta autoadhesiva emitida por la AGC
32	AFFF50-32	Etiqueta de n° de serie GS1	1	Poliéster autoadhesivo impreso térmico
34	AFFF50-34	Faja de garantía válvula-cuello	1	Vinito destructible rayado rojo/blanco
35	AFFF50-35	Precinto de fábrica	1	Polipropileno color
	AFFF50-S7	EMBALAJE		
—	AFFF50-E1	Esqueros y funda de polietileno	1 jgo	PE / cartón
—	AFFF50-E3	Pallet 1200 x 1000 (fracción)	0,5	Madera
—	AFFF50-E4	Film stretch (fracción del pallet)	0,06 kg	PE lineal 23 µm
—	AFFF50-E5	Etiqueta de pallet (lote y destino, fracción)	0,5	Papel térmico

NOTAS

- 1) Lista completa con medidas, pesos, origen, operación y norma: salida/bom/FLAMA_BOM.xlsx, hoja BOM_FL_MAT_AFFF_50l.
- 2) «-» = ítem no dibujado (internos de válvula, carga, identificación, embalaje).
- 3) S1 en los ABC = recipiente FL_REC (mismo plano que el cilindro de venta suelta).
- 4) Ruedas: se dibujan ambas, el globo señala la derecha (cantidad 2).

		Fecha	Nombre	Propietario		Reemplaza a / Reemplazado por	
Dibujó		28/09/26	T. Sinay	FLAMA S.A.		-	
Revisó						Material	
Aprobó				Denominación		Ver lista	
Escala		Método de proyección		Despiece AFFF 50 l sobre ruedas		Edición	
						0	
1:5				ISO E		Fecha de emisión	
				Vista explosionada y lista multinivel (BOM)		28/09/2026	
Tolerancias generales		Formato		Tipo de documento		Hoja	
						1 / 1	
ISO 2768-m		A2		Plano de despiece		Idioma	
						es	
						Nº de plano	
						FL_DES_AFFF_50l	