

A

B

C

D

E

F

A


B

C

D

E

F

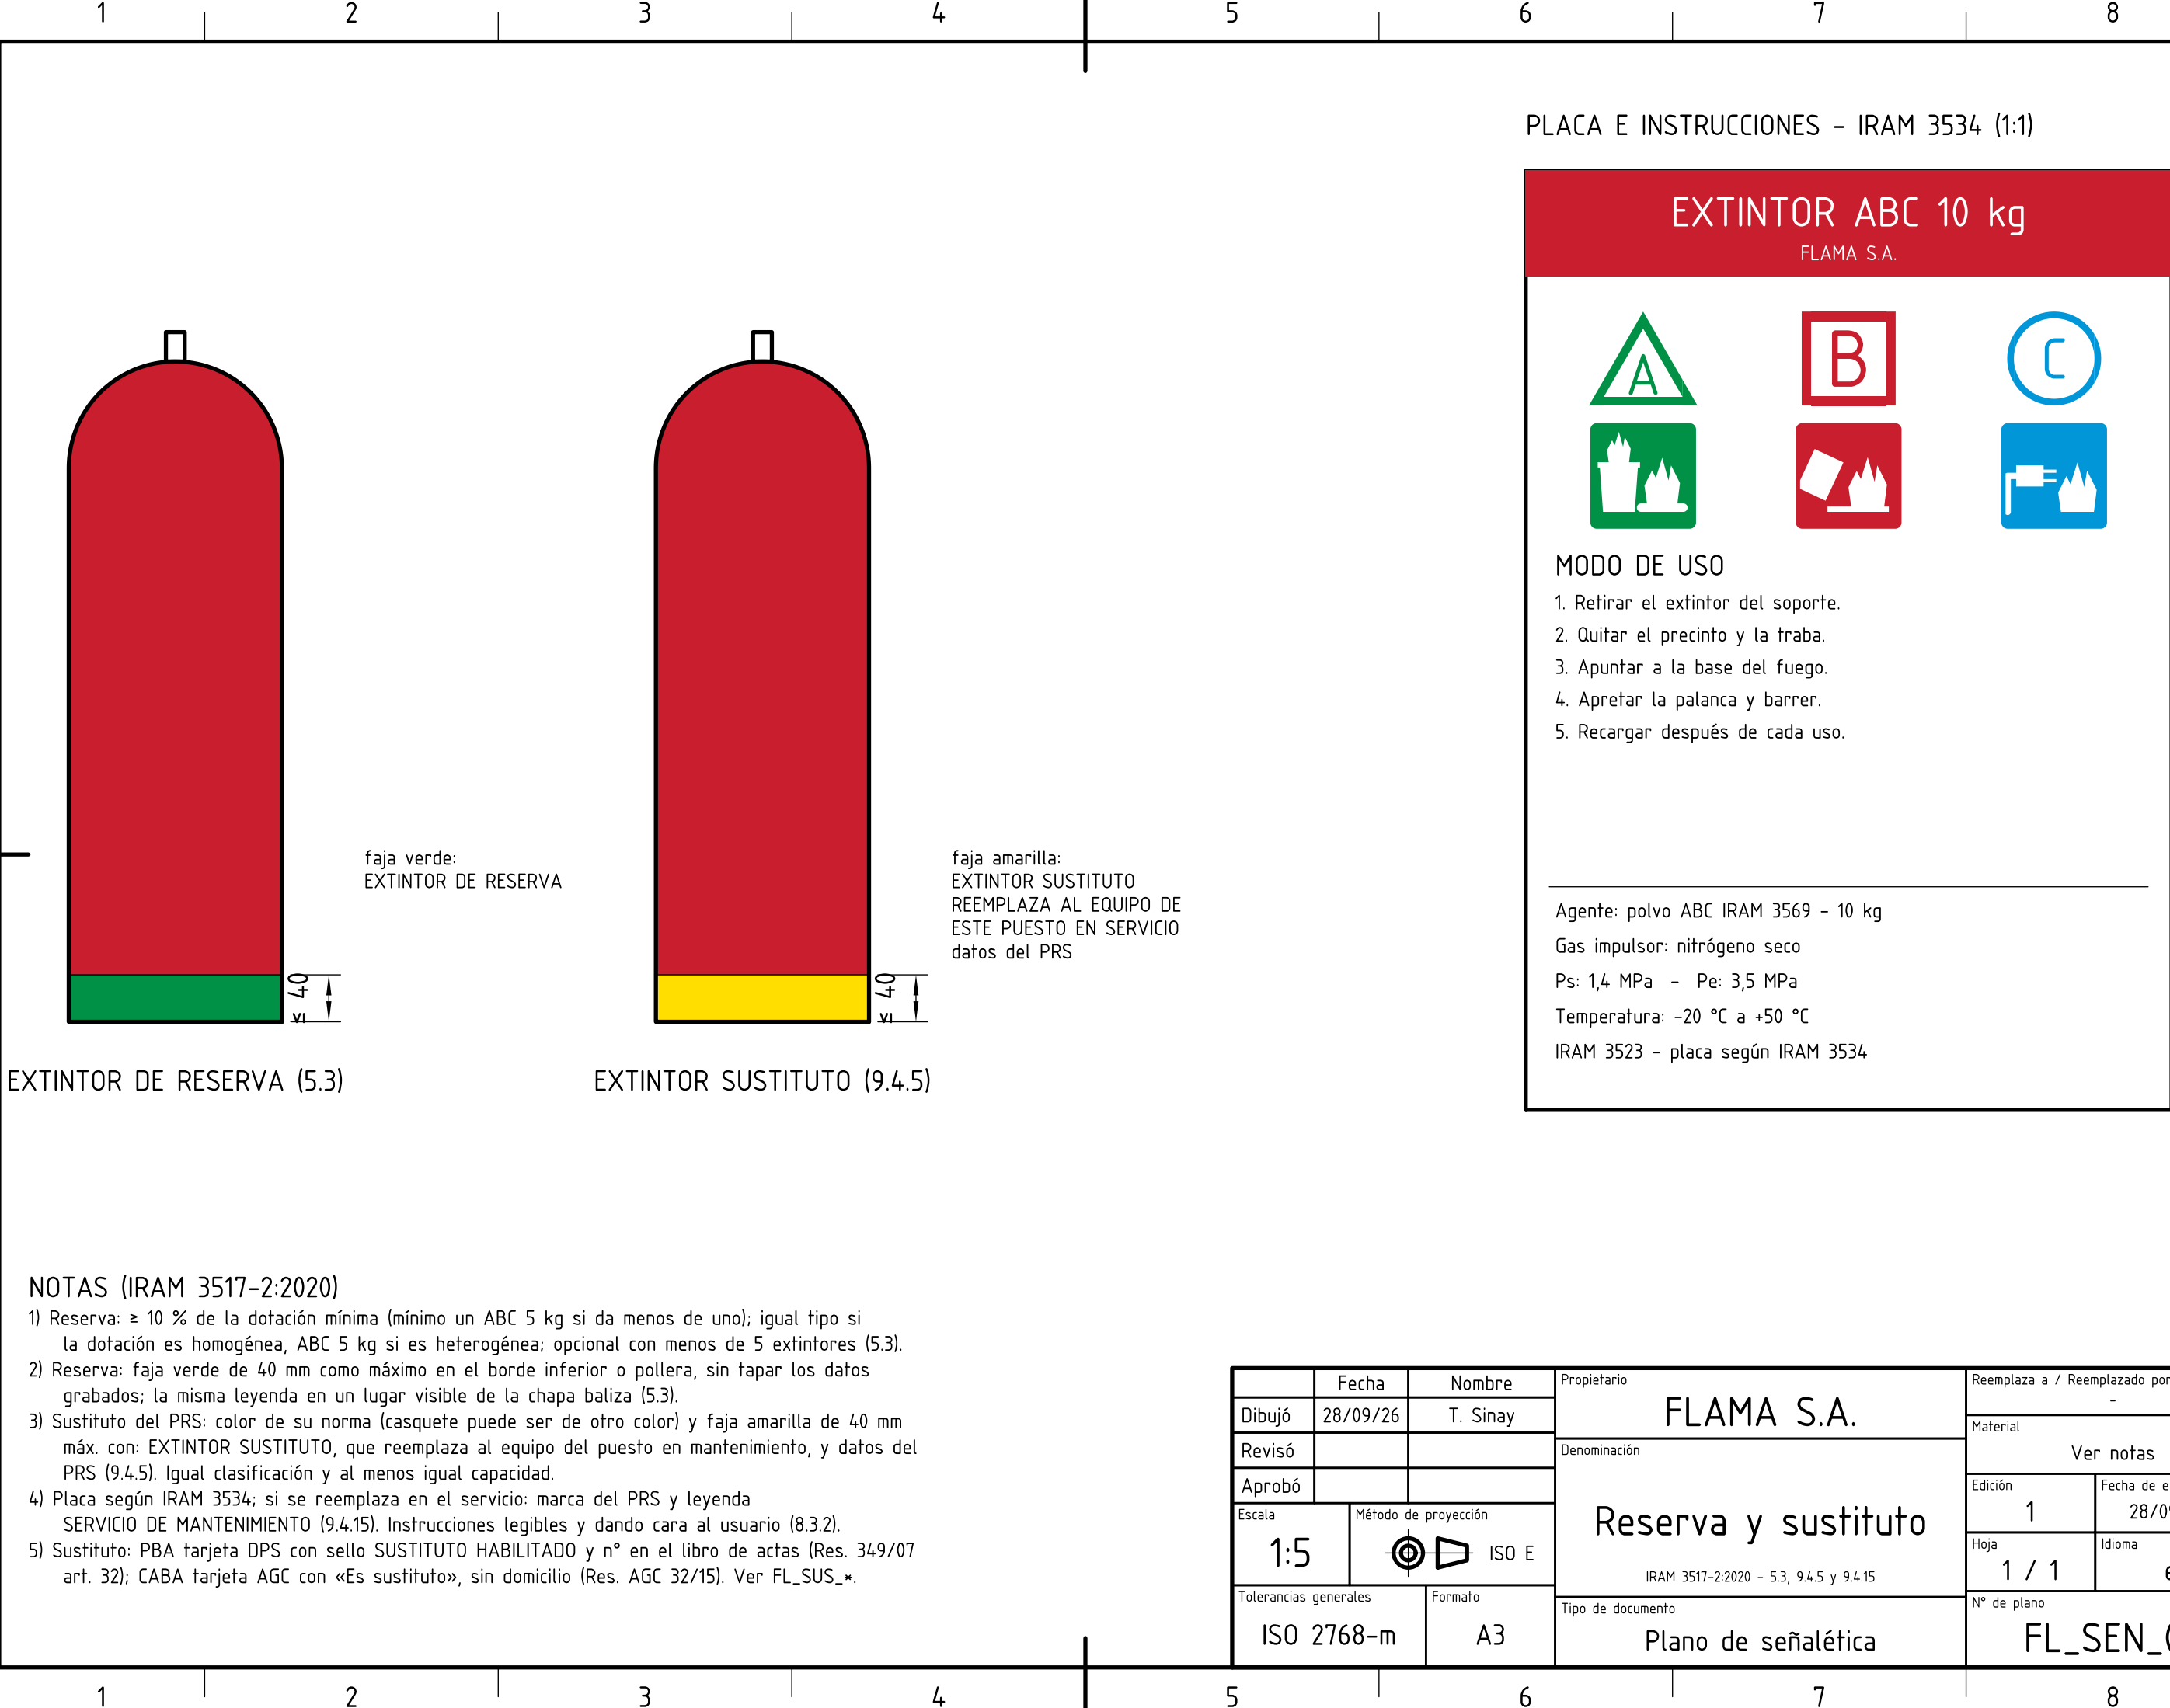

faja verde:
EXTINTOR DE RESERVA

EXTINTOR DE RESERVA (5.3)

faja amarilla:
EXTINTOR SUSTITUTO
REEMPLAZA AL EQUIPO DE
ESTE PUESTO EN SERVICIO
datos del PRS

EXTINTOR SUSTITUTO (9.4.5)

NOTAS (IRAM 3517-2:2020)

1) Reserva: $\geq 10 \%$ de la dotación mínima (mínimo un ABC 5 kg si da menos de uno); igual tipo si la dotación es homogénea, ABC 5 kg si es heterogénea; opcional con menos de 5 extintores (5.3).

2) Reserva: faja verde de 40 mm como máximo en el borde inferior o pollera, sin tapar los datos grabados; la misma leyenda en un lugar visible de la chapa baliza (5.3).

3) Sustituto del PRS: color de su norma (casquete puede ser de otro color) y faja amarilla de 40 mm máx. con: EXTINTOR SUSTITUTO, que reemplaza al equipo del puesto en mantenimiento, y datos del PRS (9.4.5). Igual clasificación y al menos igual capacidad.

4) Placa según IRAM 3534; si se reemplaza en el servicio: marca del PRS y leyenda SERVICIO DE MANTENIMIENTO (9.4.15). Instrucciones legibles y dando cara al usuario (8.3.2).

5) Sustituto: PBA tarjeta DPS con sello SUSTITUTO HABILITADO y n° en el libro de actas (Res. 349/07 art. 32); CABA tarjeta AGC con «Es sustituto», sin domicilio (Res. AGC 32/15). Ver FL_SUS_*

	Fecha	Nombre	Propietario FLAMA S.A.	Reemplaza a / Reemplazado por -	
Dibujó	28/09/26	T. Sinay		Material	
Revisó				Ver notas	
Aprobó				Edición 1	Fecha de emisión 28/09/2026
Escala 1:5		Método de proyección  ISO E	Denominación Reserva y sustituto IRAM 3517-2:2020 - 5.3, 9.4.5 y 9.4.15	Hoja 1 / 1	Idioma es
Tolerancias generales ISO 2768-m		Formato A3		N° de plano FL_SEN_06	
			Tipo de documento Plano de señalética		