

A

B

C

D

E

F

A


B

C


D

E


F

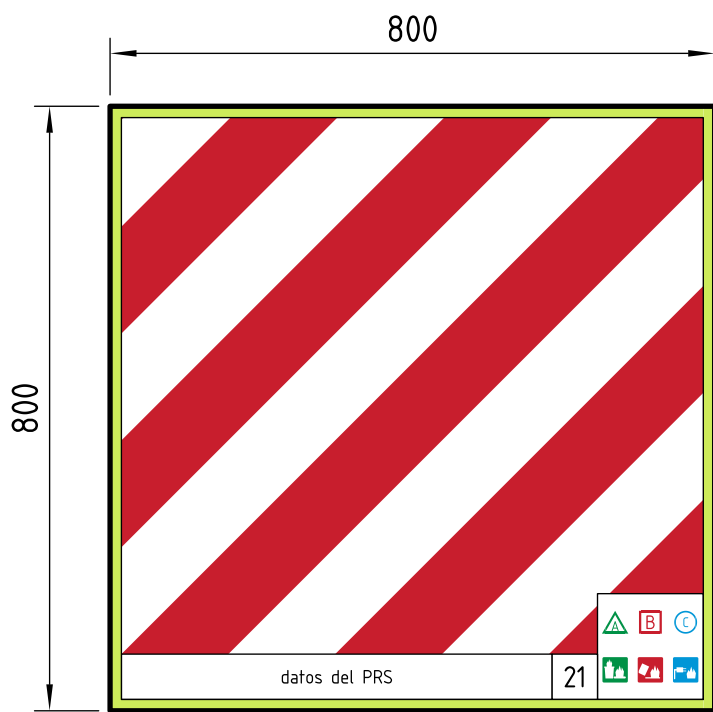


HORIZONTAL 800 × 800
(rodantes y pedestal)

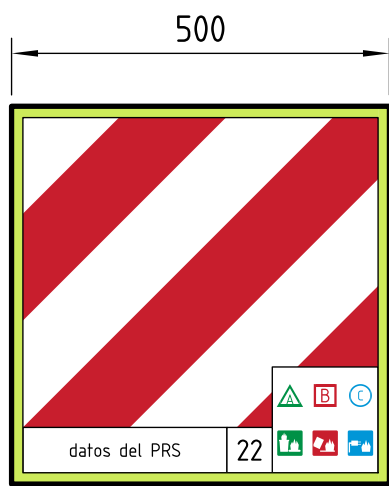

HORIZONTAL 500 × 500

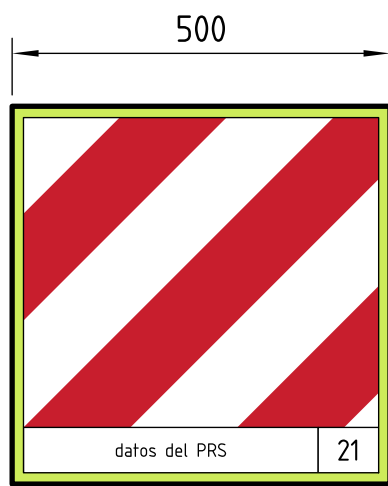

BALDES 500 × 500

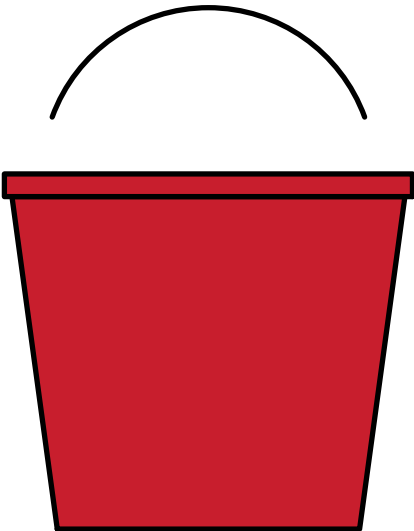

BALDE 5 a 7 L (1:5)
con tapa y manijas

NOTAS (IRAM 3517-2:2020)

- 1) Chapas horizontales o de piso para extintores rodantes y soportes pedestal: 800 × 800 ó 500 × 500, franjas rojas y blancas de 100 mm a 45° respecto de los bordes, borde fotoluminiscente de 15 mm, datos del PRS, número del puesto (60) y tipos de fuego (140 × 140) (7.2.6, figura 4).
- 2) Colores firmes y resistentes a la abrasión del tránsito y la limpieza; UV en exteriores (7.2.1).
- 3) Extintores para líquidos combustibles (garajes, grupos electrógenos, etc.): puesto con dos baldes de 5 L a 7 L, con tapa y manijas, que permitan volcar su contenido; gránulos absorbentes reemplazados anualmente en el mantenimiento del extintor (6.2.19).
- 4) Chapa de baldes 500 × 500 con datos del PRS (390) y número del puesto (80) (7.5, figura 6).
- 5) Soporte pedestal: sobre chapa horizontal, eventualmente fijado al solado (3.14).

	Fecha	Nombre	Propietario FLAMA S.A.	Reemplaza a / Reemplazado por -		
Dibujó	28/09/26	T. Sinay		Denominación Chapas de piso y baldes IRAM 3517-2:2020 - 6.2.19, 7.2.6, 7.5, figuras 4 y 6	Material Ver notas	
Revisó					Edición 1	Fecha de emisión 28/09/2026
Aprobó					Hoja 1 / 1	Idioma es
Escala 1:10		Método de proyección  ISO E		N° de plano FL_SEN_07		
Tolerancias generales ISO 2768-m		Formato A3	Tipo de documento Plano de señalética			