
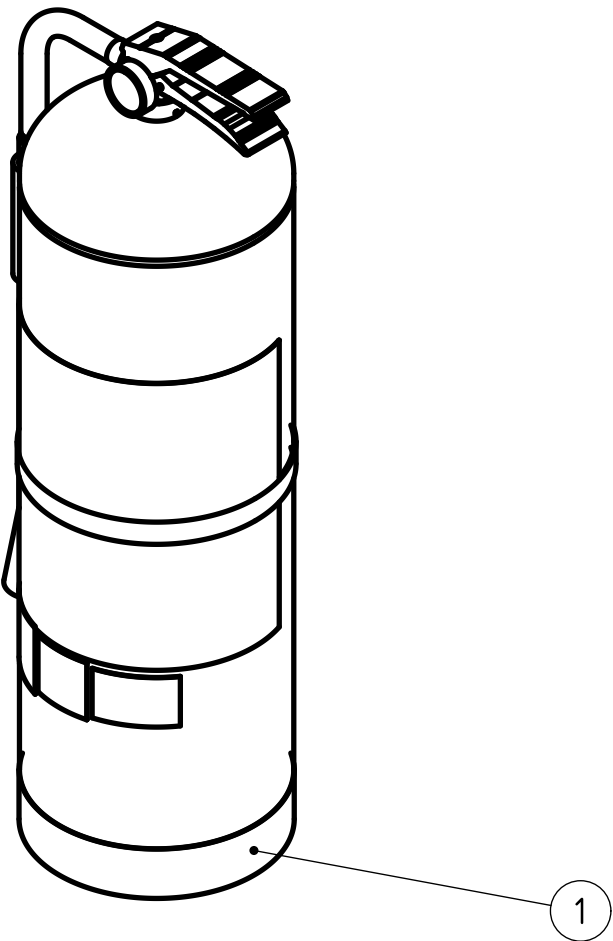


EXTINTOR SUSTITUTO PARA EXTINTOR CLASE D 9 L (IRAM 3517-2:2020 9.4.5)

ISOMETRÍA, FAJA DESPLAZADA (esc. 1:5)


VISTA ANTERIOR (esc. 1:10)

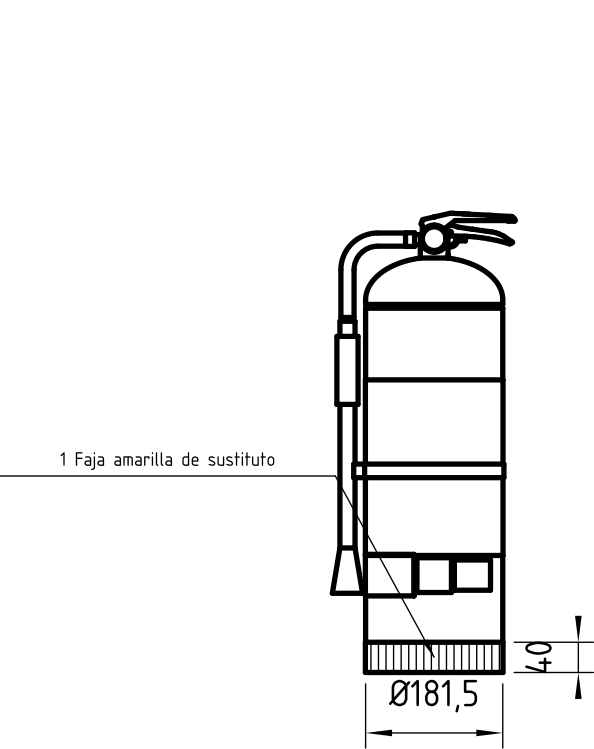

- REQUISITOS (se citan apartados):
- IRAM 3517-2:2020 9.4.5: igual clasificación y por lo menos igual capacidad que el retirado; mantenimiento vigente; color normativo (los casquetes pueden ir de otro color); faja o cinta amarilla ≤ 40 mm en la pollera con 3 leyendas.
 - Res. 349/07 art. 32 (PBA): tarjeta DPS con sello «SUSTITUTO HABILITADO», reutilizable mientras sea legible; n° del extintor en el libro de actas.
 - Res. AGC 32/15 anexo II (CABA): tarjeta con «Es sustituto», sin domicilio de instalación.
 - Remito de préstamo con membrete (práctica de mercado).
 - El sustituto conserva su placa, oblea / tarjeta y precinto; la faja no debe tapar ninguno.

Faja en el borde inferior del cuerpo (pollera), alto 40 mm (≤ 40 , sin tapar la oblea PBA); rodea todo el perímetro.

DETALLE 1 - DESARROLLO DE LA FAJA 40 × 590 (esc. 1:2) - amarillo; leyendas negras repetidas

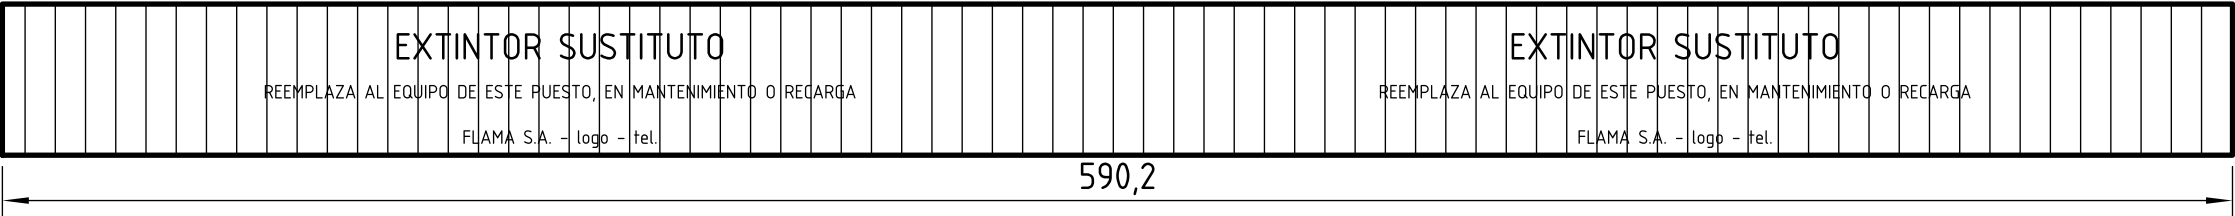

LISTA - BOM FL_SUS_CLASED_9L			
Glo.	Código BOM	Denominación	Cant.
1	SUS-CLASED_9L-01	Faja amarilla de sustituto 40 × 590	1
–	SUS-CLASED_9L-02	Tarjeta DPS con sello «SUSTITUTO HABILITADO» (PBA)	1
–	SUS-CLASED_9L-03	Tarjeta AGC «Es sustituto» (CABA)	1
–	SUS-CLASED_9L-04	Remito de préstamo con membrete	1/préstamo
–	FL_MAT_CLASED_9L	Extintor base del mismo modelo (BOM: hoja FL_MAT_CLASED_9L)	1

	Fecha	Nombre	Propietario FLAMA S.A.	Reemplaza a / Reemplazado por -	
Dibujó	28/09/26	T. Sinay		Material	
Revisó				Ver lista	
Aprobó				Edición 0	Fecha de emisión 28/09/2026
Escala 1:10		Método de proyección  ISO E		Hoja 1 / 1	
Tolerancias generales ISO 2768-m		Formato A3	Identificación sobre Clase D 9 l Tipo de documento Extintor sustituto	Idioma es	
				N° de plano FL_SUS_CLASED_9l	

Clasificación D · alternativa admisible: -