

EXTINTOR SUSTITUTO PARA EXTINTOR AGUA 10 L (IRAM 3517-2:2020 9.4.5)

VISTA ANTERIOR (esc. 1:10)

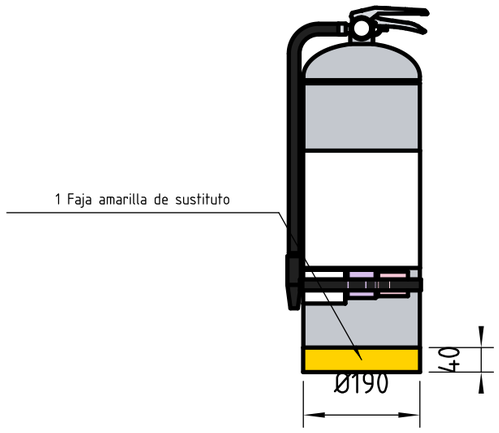

ISOMETRÍA, FAJA DESPLAZADA (esc. 1:5)

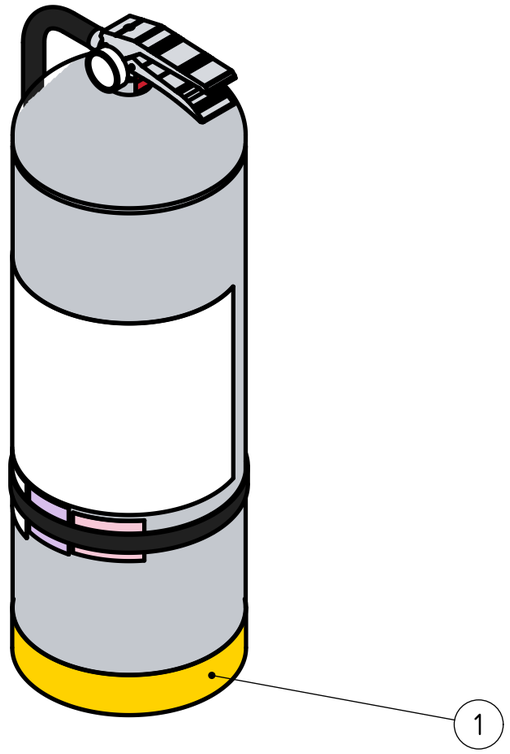

REQUISITOS (se citan apartados):

- IRAM 3517-2:2020 9.4.5: igual clasificación y por lo menos igual capacidad que el retirado; mantenimiento vigente; color normativo (los casquetes pueden ir de otro color); faja o cinta amarilla ≤ 40 mm en la pollera con 3 leyendas.
- Res. 349/07 art. 32 (PBA): tarjeta DPS con sello «SUSTITUTO HABILITADO», reutilizable mientras sea legible; n° del extintor en el libro de actas.
- Res. AGC 32/15 anexo II (CABA): tarjeta con «Es sustituto», sin domicilio de instalación.
- Remito de préstamo con membrete (práctica de mercado).
- El sustituto conserva su placa, oblea / tarjeta y precinto; la faja no debe tapar ninguno.

Faja en el borde inferior del cuerpo (pollera), alto 40 mm (≤ 40, sin tapar la oblea PBA); rodea todo el perímetro.

DETALLE 1 - DESARROLLO DE LA FAJA 40 × 617 (esc. 1:2) - amarillo; leyendas negras repetidas

EXTINTOR SUSTITUTO
REEMPLAZA AL EQUIPO DE ESTE PUESTO, EN MANTENIMIENTO O RECARGA
FLAMA S.A. - logo - tel.

EXTINTOR SUSTITUTO
REEMPLAZA AL EQUIPO DE ESTE PUESTO, EN MANTENIMIENTO O RECARGA
FLAMA S.A. - logo - tel.

616,9

LISTA - BOM FL_SUS_AGUA_10l

Glo.	Código BOM	Denominación	Cant.
1	SUS-AGUA_10l-01	Faja amarilla de sustituto 40 × 617	1
–	SUS-AGUA_10l-02	Tarjeta DPS con sello «SUSTITUTO HABILITADO» (PBA)	1
–	SUS-AGUA_10l-03	Tarjeta AGC «Es sustituto» (CABA)	1
–	SUS-AGUA_10l-04	Remito de préstamo con membrete	1/préstamo
–	FL_MAT_AGUA_10l	Extintor base del mismo modelo (BOM: hoja FL_MAT_AGUA_10l)	1

	Fecha	Nombre
Dibujó	28/09/26	T. Sinay
Revisó		
Aprobó		

Escala: 1:10
Método de proyección: ISO E
Tolerancias generales: ISO 2768-m
Formato: A3

Propietario: FLAMA S.A.
Denominación: Extintor sustituto
Identificación sobre Agua 10 l
Tipo de documento: Extintor sustituto

Reemplaza a / Reemplazado por: -
Material: Ver lista
Edición: 0
Fecha de emisión: 28/09/2026
Hoja: 1 / 1
Idioma: es
N° de plano: FL_SUS_AGUA_10l

Clasificación A · alternativa admisible: -