

A

B

C

D

E

F

A


B

C

D

E

F

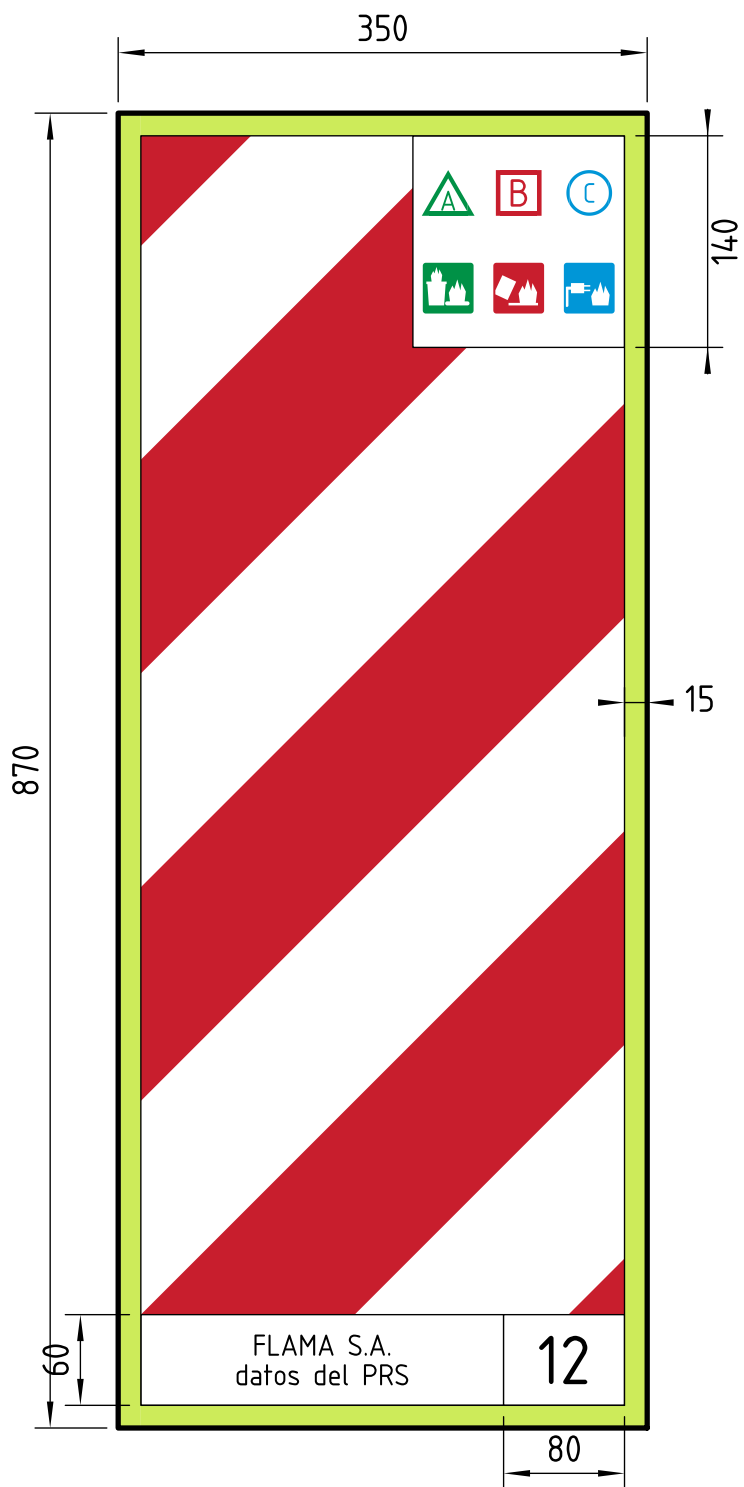


CHAPA 350 × 870 (preferente)



CHAPA 260 × 870
(sólo si no entra la de 350)

NOTAS (IRAM 3517-2:2020)

- 1) Franjas rojas y blancas de 100 mm a 45°; borde fotoluminiscente de 15 mm (7.2.1, 7.2.5).
- 2) Contenido obligatorio: tipos de fuego (letra + pictograma, FL_SEN_03), número del puesto y datos del prestador que instaló (7.2.1 a 7.2.4). Numeración del extintor: FL_SEN_04.
- 3) Se instala siempre la de 350 mm; la de 260 mm sólo cuando el muro o la columna no lo permite.
- 4) Extintor de hasta 20 kg: parte superior a $\leq 1,5$ m; de más de 20 kg: $\leq 1,0$ m; siempre $\geq 0,10$ m libre entre su base y el piso (6.2.14). Nunca en rampas ni escaleras (6.2.18).
- 5) Cartel en altura a 2,0 m – 2,5 m sobre la vertical de la baliza (7.3). Colores s/ IRAM-DEF D 1054.
- 6) Chapa de PAI o aluminio con tratamiento UV para exterior; colores firmes y resistentes a la limpieza.
- 7) La norma no fija la altura de la chapa: se ubica detrás del extintor, visible por encima de él.

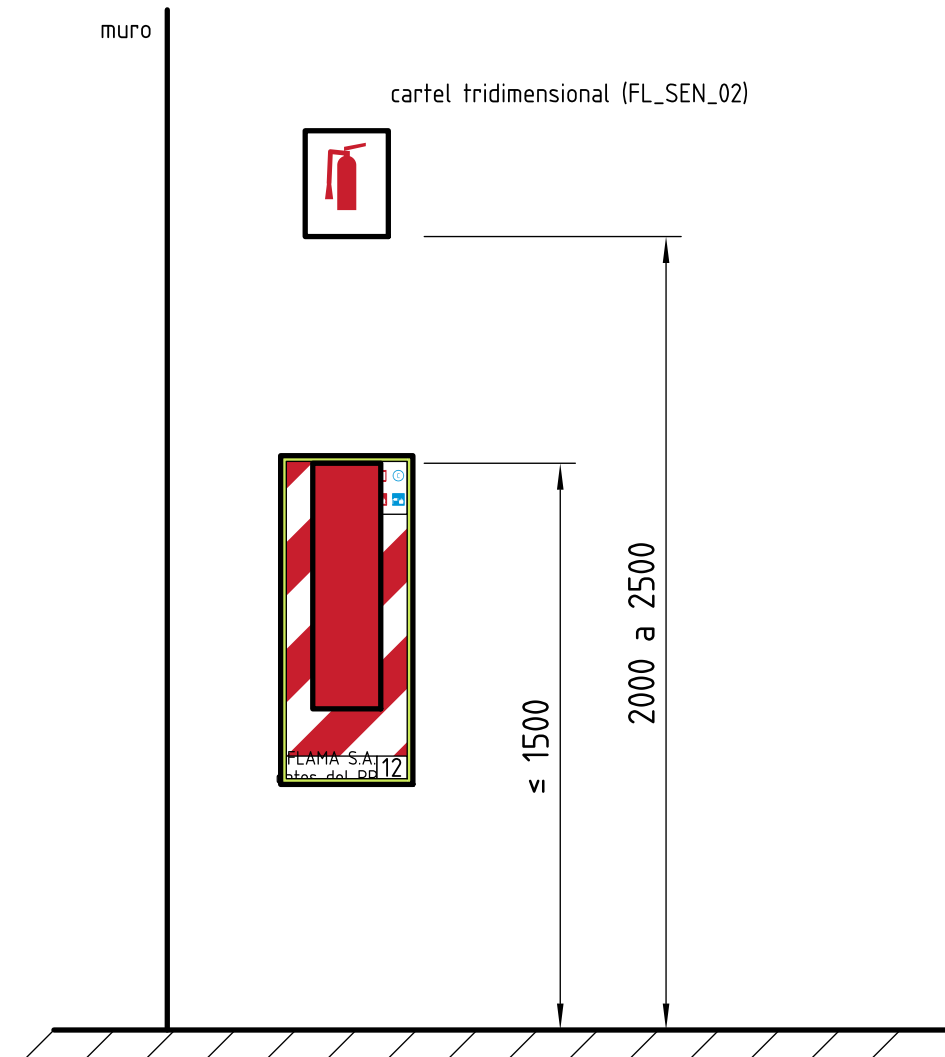

PUESTO DE INCENDIO (1:20)

	Fecha	Nombre	Propietario	Reemplaza a / Reemplazado por	
Dibujó	28/09/26	T. Sinay	FLAMA S.A.	-	
Revisó			Denominación	Ver notas	
Aprobó			Chapa baliza vertical IRAM 3517-2:2020 - 7.2.1, 7.2.5 y figura 3	Edición	Fecha de emisión
Escala		Método de proyección		1	28/09/2026
1:5		 ISO E		Hoja	Idioma
Tolerancias generales		Formato	Tipo de documento	1 / 1	es
ISO 2768-m		A3		Nº de plano	FL_SEN_01
			Plano de señalética		