

A

B

C

D

E

F

G

H

J


K

L

M

DESPIECE - EXTINTOR ABC 50 KG SOBRE RUEDAS

Isometría explosionada por subconjunto, escala 1:5. Globo = posición del plano FL_MAT_ABC_50kg = código ABC50-NN

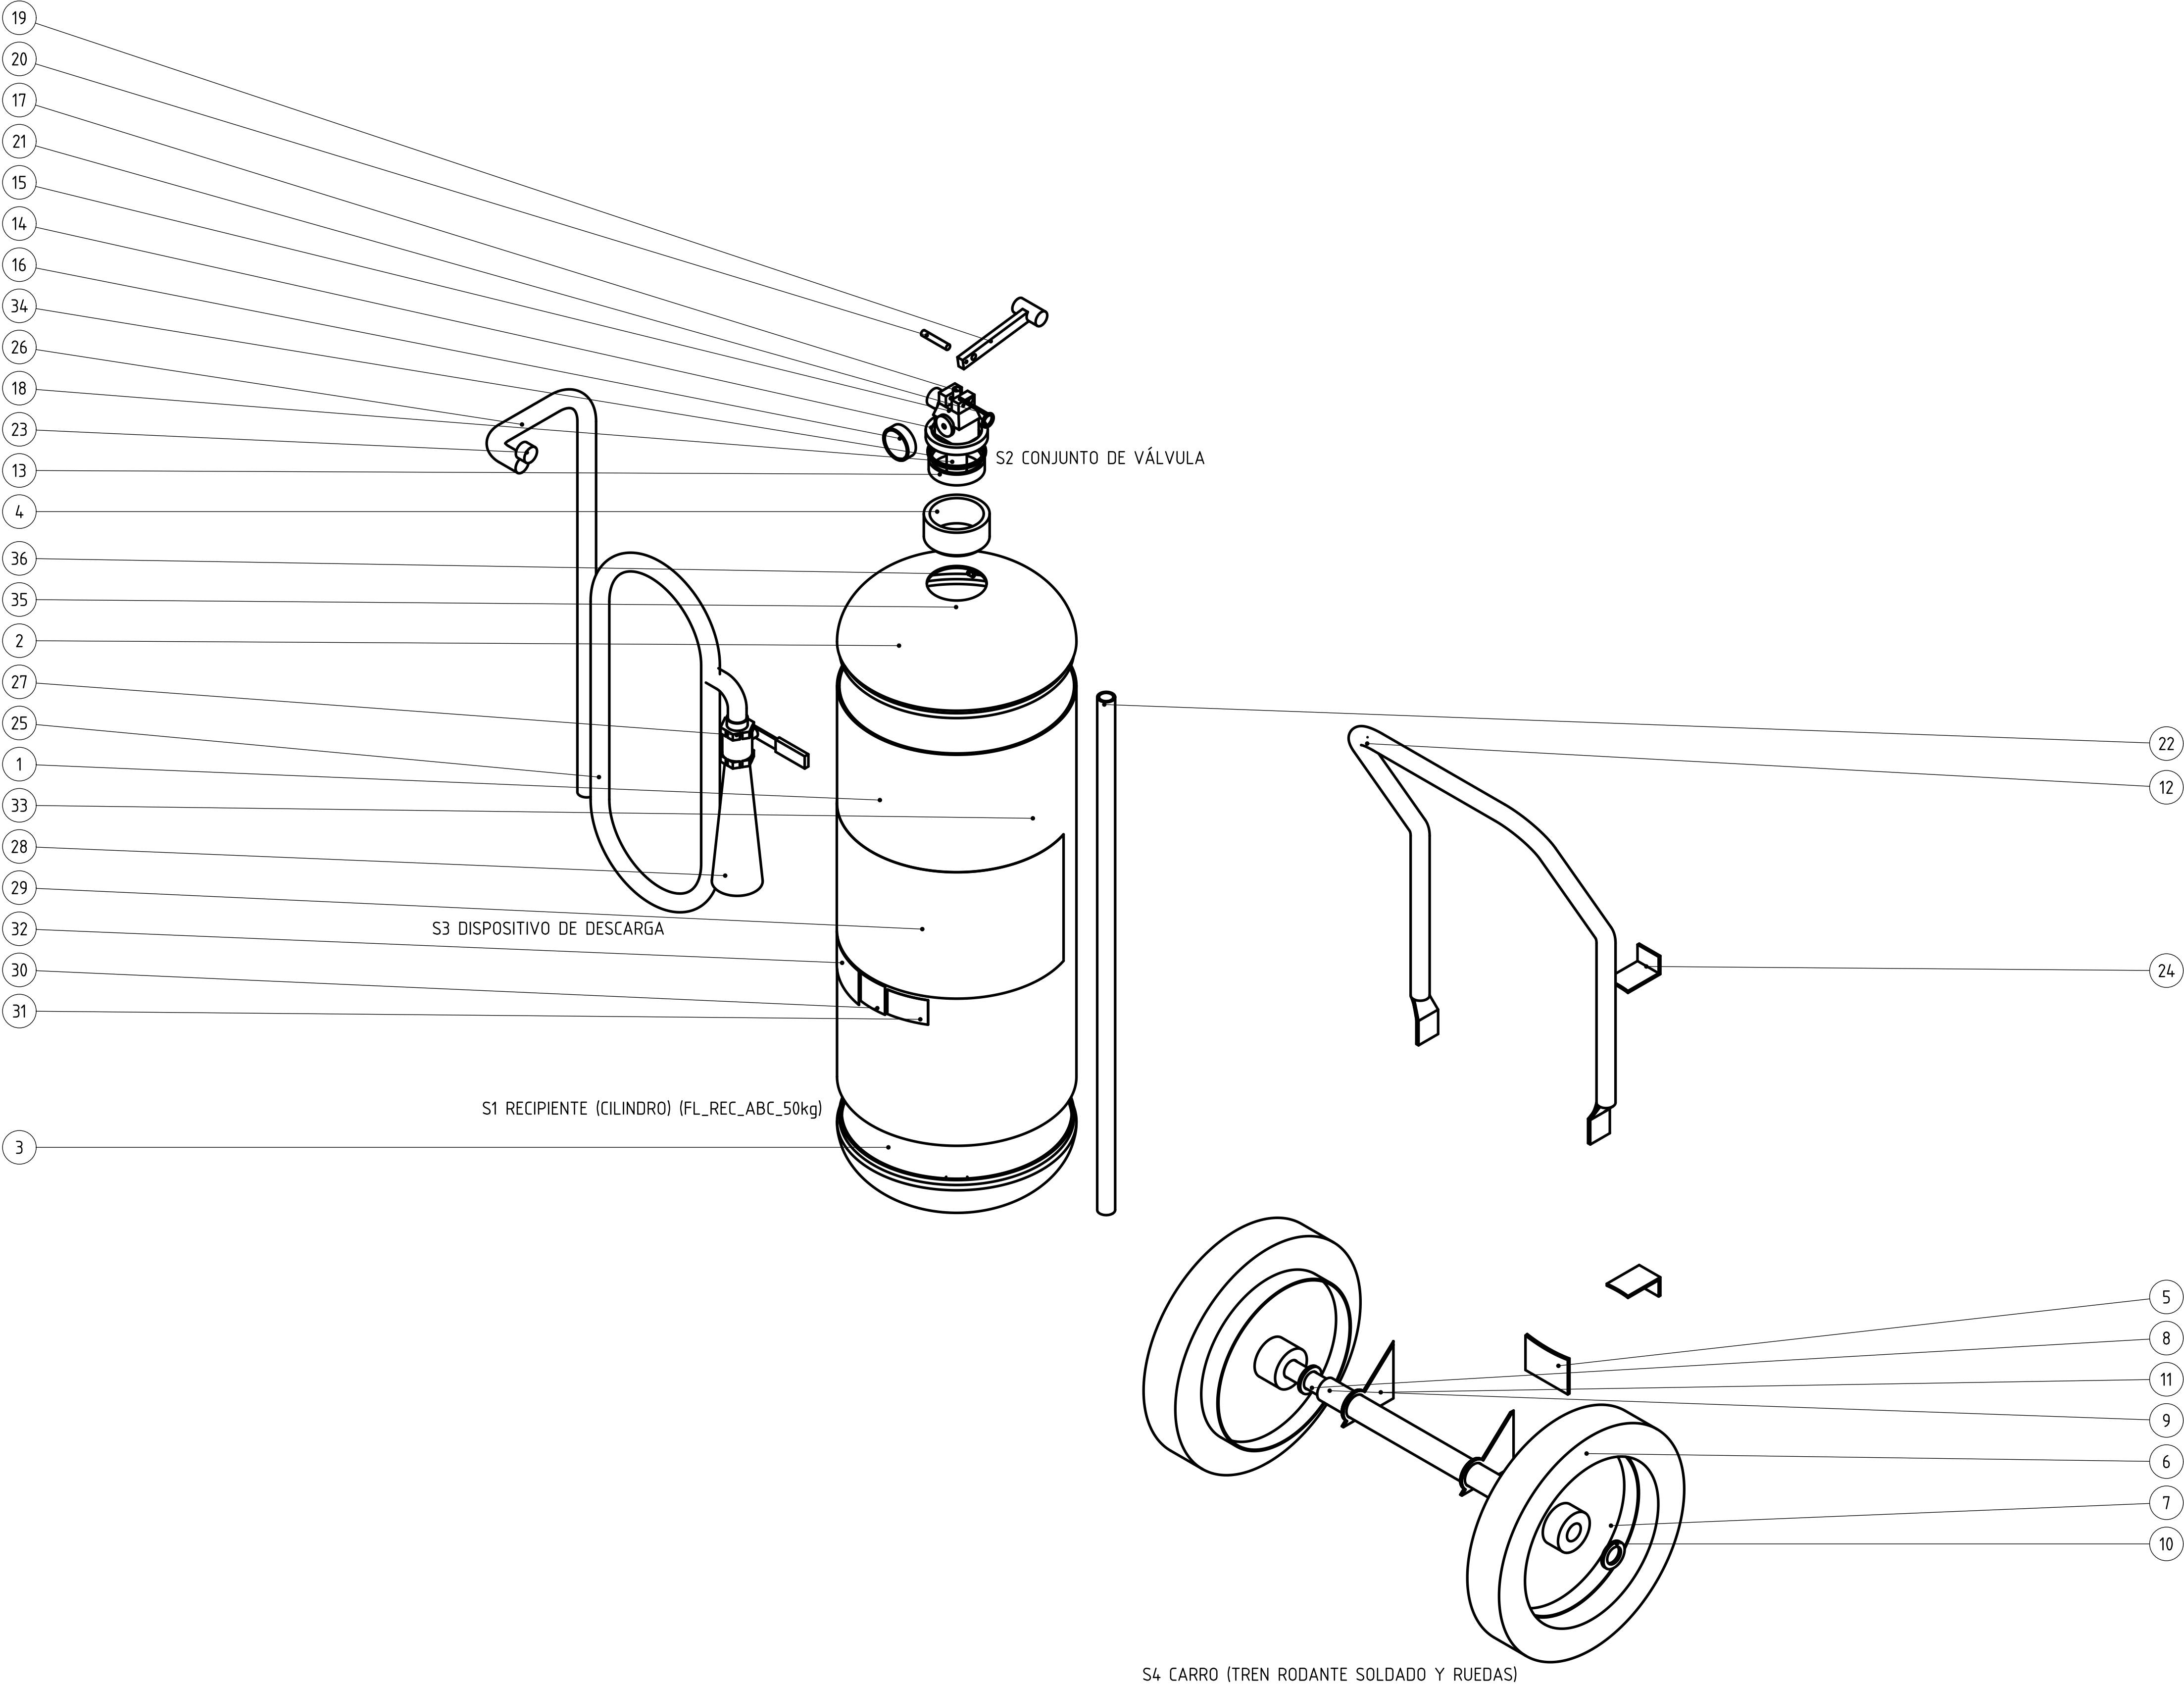

LISTA DE DESPIECE - BOM FL_MAT_ABC_50kg				
Glo.	Código BOM	Denominación	Cant.	Material
—	FL_REC_ABC_50kg	RECIPIENTE (CILINDRO)		
1	ABC50-01	Cuerpo (vital)	1	Chapa LAC IRAM-IAS U 500-04 e=3,2
2	ABC50-02	Cúpula	1	Chapa LAC IRAM-IAS U 500-04 e=3,2
3	ABC50-03	Fondo	1	Chapa LAC IRAM-IAS U 500-04 e=3,2
4	ABC50-04	Cuello roscado	1	Acero SAE 1010
—	ABC50-01	Alambre MAG ERT05-6 Ø10 (AWS A5.18)	0,4262 kg	ERT05-6
—	ABC50-02	Gas de protección MAG Arca 21 / ARCAL Speed (Ar + 8 % CO2, M20)	68,3 L	EN ISO 14175 M20-Arc-8
—	ABC50-04	Servicio de pintura en polvo al horno, rojo 03-1-050 (con preparación por succion)	1	Servicio ferrerizado
—	ABC50-02	CONJUNTO DE VÁLVULA		
13	ABC50-13	Esfera roscada	1	Latón forjado
14	ABC50-14	Collarín de válvula	1	Latón forjado
15	ABC50-15	Cuerpo de válvula	1	Latón forjado
16	ABC50-16	Manómetro	1	Comercial
17	ABC50-17	Vástago	1	Latón
18	ABC50-18	Resorte de válvula	1	Alambre acero inox. AISI 302
19	ABC50-19	Palanca de accionamiento	1	Planchuela acero SAE 1010 10 x 16 pintada
20	ABC50-20	Eje de palanca	1	Acero inox. AISI 304
21	ABC50-21	Pasador de seguridad	1	Alambre acero inox. AISI 304
22	ABC50-22	Cabo de pesca (sifón)	1	Tubo PVC rígido
34	ABC50-34	Junta tórica de asiento	1	NBR 70 Shore A
—	ABC50-K2	Válvula H2 armada de carro 50-70-100 kg	1	Latón forjado (H2)
—	ABC50-V2	Resorte de retorno del vástago	1	Acero para resortes
—	ABC50-V3	Junta tórica del vástago	1	NBR 70 Shore A
—	ABC50-03	DISPOSITIVO DE DESCARGA		
23	ABC50-23	Racor de manguera	1	Latón
25	ABC50-25	Manguera (tramo enrollado)	1	Caucho sintético
26	ABC50-26	Manguera	1	Caucho sintético
27	ABC50-27	Válvula esférica	1	Latón cromado
28	ABC50-28	Tobera campana	1	Polipropileno
—	ABC50-04	CARRO (TREN RODANTE SOLDADO Y RUEDAS)		
5	ABC50-05	Tercera pala	1	Chapa LAC 3,2 (lorilla de la hoja de 25 kg)
6	ABC50-06	Neumático macizo	2	Caucho
7	ABC50-07	Llanta con cubo	2	Chapa acero SAE 1010
8	ABC50-08	Eje de ruedas	1	Barra acero SAE 1045 Ø25
9	ABC50-09	Portaje	1	Cable acero SAE 1010 Ø33,7 x 3,25
10	ABC50-10	Arandelas de tope (4)	1	Acero SAE 1010 Ø40 x Ø26 x 4
11	ABC50-11	Chapas triangulares del portaje (2)	1	Chapa LAC del cuerpo (lorilla)
12	ABC50-12	Manija del carro	1	Cable acero SAE 1010 Ø25,4x1,6
24	ABC50-24	Ganchos portamanguera (2)	1	Chapa LAC del cuerpo (lorilla) plegada
—	ABC50-05	CARGA: AGENTE EXTINTOR Y GAS IMPULSOR		
—	ABC50-A1	Pulvo químico seco ABC 90 (Sello IRAM 3569)	50 kg	Pulvo químico seco ABC 90 (Sello IRAM 3569)
—	ABC50-A2	Gas impulsor: N2	0,2819 kg	N2
—	ABC50-06	IDENTIFICACIÓN Y PRECINTO		
29	ABC50-29	Etiqueta / placa de características	1	Vinilo autoadhesivo laminado
30	ABC50-30	Órdea de fabricación (IPRA)	1	Papel de seguridad autodestructible
31	ABC50-31	Estrangillo IRAM de conformidad	1	Provisio por IRAM (Anexo R)
32	ABC50-32	Tarjeta de identificación AGC (CABA)	1	Etiqueta autoadhesiva emitida por la AGC
33	ABC50-33	Etiqueta de n° de serie GS1	1	Poliéster autoadhesivo impreso térmico
35	ABC50-35	Faja de garantía válvula-cuello	1	Vinilo destructible rayado rojo/blanco
36	ABC50-36	Precinto de fábrica	1	Polipropileno color
—	ABC50-07	EMBALAJE		
—	ABC50-E1	Esqueros y funda de polietileno	1 jgo	PE / cartón
—	ABC50-E3	Pallet 1200 x 1000 (fracción)	0,5	Madera
—	ABC50-E4	Film stretch (fracción del pallet)	0,06 kg	PE lineal 23 µm
—	ABC50-E5	Etiqueta de pallet lote y destino, fracción	0,5	Papel térmico

NOTAS

1) Lista completa con medidas, pesos, origen, operación y norma: salida/bom/FLAMA_BOM.xlsx, hoja BOM_FL_MAT_ABC_50kg.

2) «-» = ítem no dibujado (internos de válvula, carga, identificación, embalaje).

3) S1 en los ABC = recipiente FL_REC (mismo plano que el cilindro de venta suelta).

4) Ruedas: se dibujan ambas, el globo señala la derecha (cantidad 2).

	Fecha	Nombre	Propietario	Reemplaza a / Reemplazado por	
Dibujó	28/09/26	T. Sinay	FLAMA S.A.		Material
Revisó			Denominación		Ver lista
Aprobó			Despiece ABC 50 kg sobre ruedas		Edición
Escala	1:5	Método de proyección			0
			Vista explosionada y lista multinivel (BOM)		Fecha de emisión
					28/09/2026
					Hoja
					1 / 1
					Idioma
					es
					N° de plano
					FL_DES_ABC_50kg
Tolerancias generales		Forma	Tipo de documento		
ISO 2768-m		A1	Plano de despiece		