


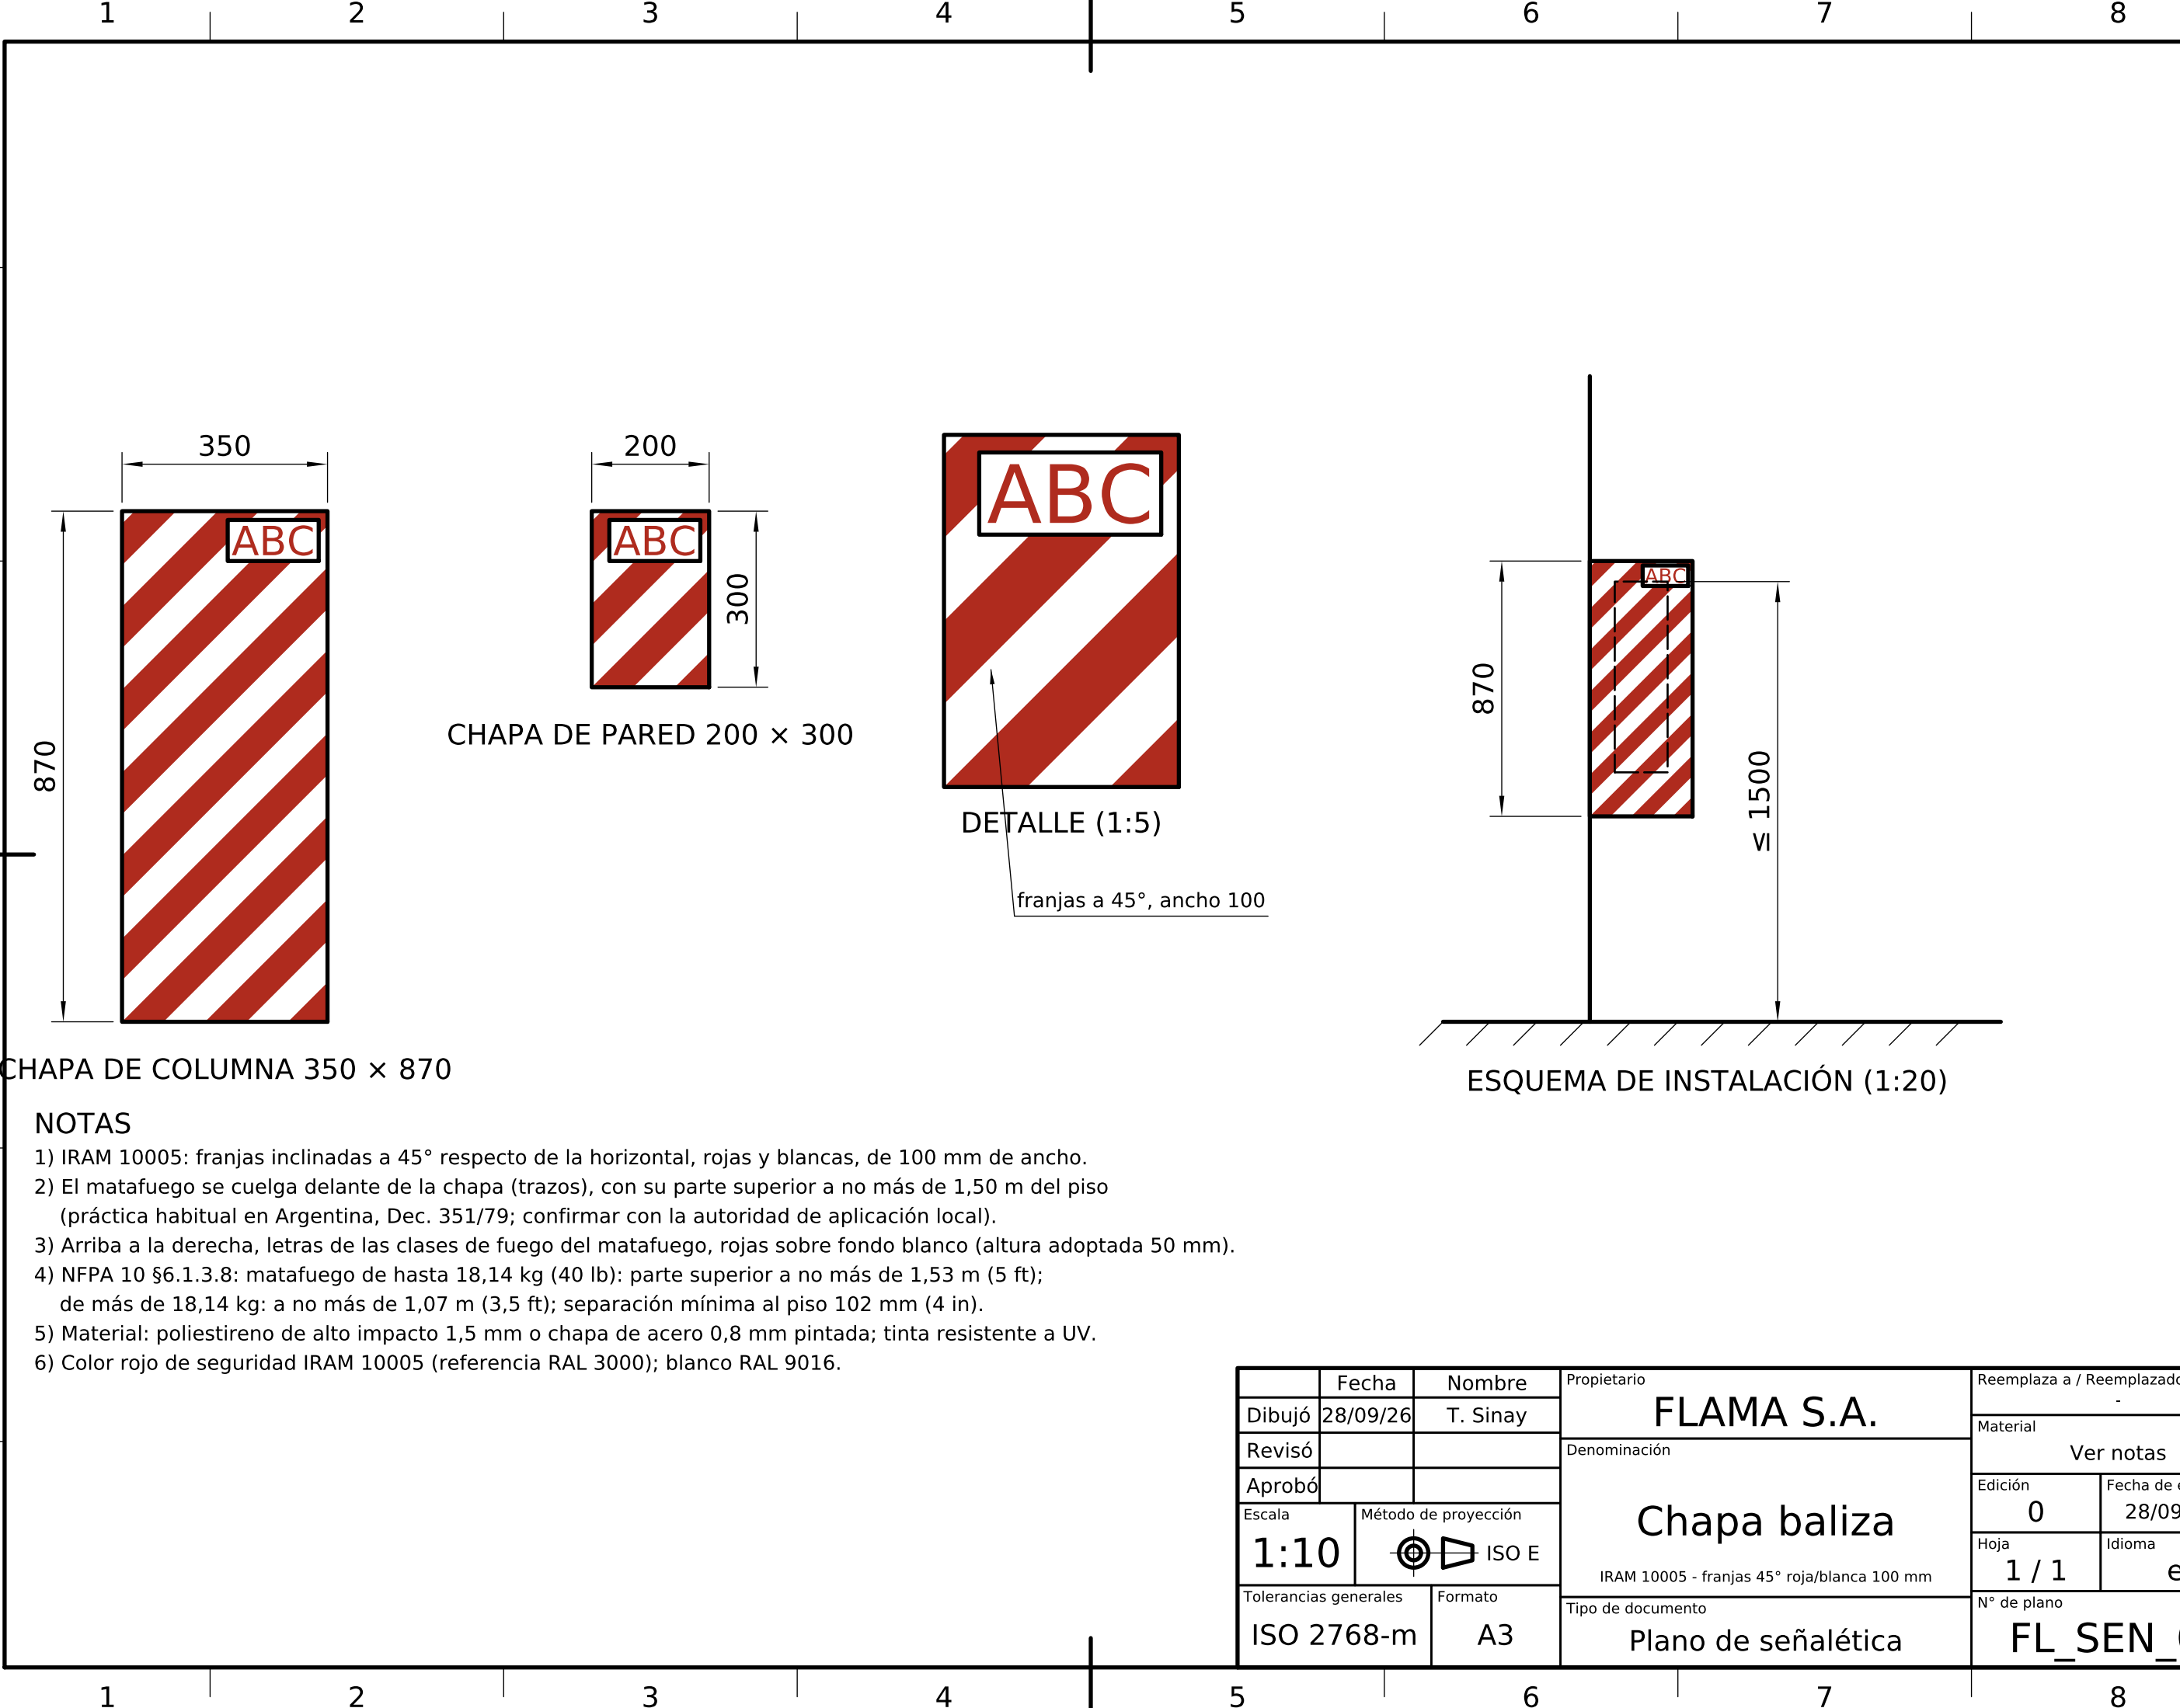

CHAPA DE COLUMNA 350 × 870

CHAPA DE PARED 200 × 300

DETALLE (1:5)

ESQUEMA DE INSTALACIÓN (1:20)

NOTAS

- 1) IRAM 10005: franjas inclinadas a 45° respecto de la horizontal, rojas y blancas, de 100 mm de ancho.
- 2) El matafuego se cuelga delante de la chapa (trazos), con su parte superior a no más de 1,50 m del piso (práctica habitual en Argentina, Dec. 351/79; confirmar con la autoridad de aplicación local).
- 3) Arriba a la derecha, letras de las clases de fuego del matafuego, rojas sobre fondo blanco (altura adoptada 50 mm).
- 4) NFPA 10 §6.1.3.8: matafuego de hasta 18,14 kg (40 lb): parte superior a no más de 1,53 m (5 ft); de más de 18,14 kg: a no más de 1,07 m (3,5 ft); separación mínima al piso 102 mm (4 in).
- 5) Material: poliestireno de alto impacto 1,5 mm o chapa de acero 0,8 mm pintada; tinta resistente a UV.
- 6) Color rojo de seguridad IRAM 10005 (referencia RAL 3000); blanco RAL 9016.

	Fecha	Nombre	Propietario FLAMA S.A.		Reemplaza a / Reemplazado por -	
Dibujó	28/09/26	T. Sinay			Material	
Revisó			Denominación Chapa baliza IRAM 10005 - franjas 45° roja/blanca 100 mm		Ver notas	
Aprobó					Edición 0	Fecha de emisión 28/09/2026
Escala 1:10	Método de proyección  ISO E				Hoja 1 / 1	Idioma es
Tolerancias generales ISO 2768-m		Formato A3			Tipo de documento Plano de señalética	